



ТехноВектор

ООО «ТехноВектор»

Юридический адрес: г. Тюмень,

ул. Ветеранов труда, 34А

ОГРН 1177232002067

Тел: +7 3452 66 28 27, +7982 906 92 27

ИНН/КПП 7203408581/720301001

Здание мобильное МЗ-22 30100x27100x10180

Учебно-тренинговый центр

РАБОЧАЯ ДОКУМЕНТАЦИЯ

«Архитектурные решения»

02-26 МЗ-УТЦ АР



ТехноВектор

ООО «ТехноВектор»

Юридический адрес: г. Тюмень,

ул. Ветеранов труда, 34А

ОГРН 1177232002067

Тел: +7 3452 66 28 27, +7982 906 92 27

ИНН/КПП 7203408581/720301001

Здание мобильное МЗ-22 30100x27100x10180

Учебно-тренинговый центр

РАБОЧАЯ ДОКУМЕНТАЦИЯ

«Архитектурные решения»

02-26 МЗ-УТЦ АР

Генеральный директор

Хамуряк А.В.

Согласовано

Взам. инв. №

Подп. и дата

Инв. № подл.

Мобильное здание учебно-тренинговый центр, одноэтажное. Размер здания в плане по осям составляет 30100 x 27100 мм.

Согласно СП 20.13330.2016 "Нагрузки и воздействия" и СП 131.13330.2020 "Строительная климатология" для расчета приняты следующие характеристики района строительства:

- температура наиболее холодных суток с обеспеченностью 0,98 – минус 42 С°;
- температура наиболее холодной пятидневки обеспеченностью 0,98 – минус 44 С°;
- вес снегового покрова для IV района согласно СП 20.13330.2016 (приложение Ж карта 1) при нормативной нагрузке составляет 2,0 кПа (табл. 10.1);
- нормативное значение ветрового давления для I района согласно СП 20.13330.2016 (прил. Ж карта 3) составляет 0,23кПа (табл.11.1).

Мобильное здание – IV степени огнестойкости.

Класс конструктивной пожарной опасности – CO,

Класс функциональной пожарной опасности здания – Ф4.2.

Мобильное здание представляет соединённые между собой блок-контейнеры, опирающиеся на подрамник. Каждый блок-контейнер имеет систему вертикальных и горизонтальных связей, обеспечивающих жёсткость каркаса.

В продольном направлении устойчивость мобильного здания обеспечивается жесткостью стоек, системой вертикальных и горизонтальных связей блоков, в поперечном направлении – жесткостью стоек, системой вертикальных и горизонтальных связей блоков.

Фундамент под мобильное здание запроектирован плитный из дорожных плит ПДН-14.

За относительную отметку 0,000 принята отметка верха чистого пола.

Все помещения здания подразделены по функциональному назначению.

Установку дверных блоков производить в соответствии ГОСТ 34378-2018.

Наружные двери оснащены устройствами без ключевого доступа.

Над каждой наружной дверью для защиты от осадков предусмотрен козырёк. Чертежи на козырёк см. раздел КР.

Для проветривания тех. подполья запроектированы решетки в каждом торце здания. Чертежи на решетки см. раздел КР.

Установку окон производить в соответствии ГОСТ 30971-2012.

Применяемые сэндвич-панели должны соответствовать ГОСТ 32603-2021 "Панели трехслойные с металлическими облицовками и сердечником из минеральной ваты".

В качестве напольного покрытия в здании мобильного здания используется линолеум коммерческий, в сан узле керамогранит.

Производство работ по антикоррозионной защите вести в соответствии с требованиями СП 72.13330.2016 "Защита строительных конструкций и сооружений от коррозии". Подготовку металлоконструкций, защиту и покрытие производить согласно указаниям ГОСТ 9.402-2005.

Все металлические конструкции защитить антикоррозионным покрытием в соответствии с требованиями СП 28.13330.2012. Перед нанесением антикоррозионного покрытия металлические поверхности подлежат зачистке, очистке от пыли и обезжириванию.

Для металлоконструкций которые не подлежат обработке огнезащиты предусмотрено покрытие грунт толщиной 50 мкм и в качестве покрывного слоя применить материал с толщиной от 70 до 100 мкм. Общий слой покрытия 120-150 мкр. * по мере необходимости

Каркасом мобильного здания является стальная металлоконструкция, выполненная с использованием сварных соединений.

Кровля мобильного здания выполнена из профилированных лист НС 44, смонтированной на стальной раме.

Профилированный лист НС 44, имеет непрерывный электрический контакт с заземлённым каркасом мобильного здания.

Таким образом, кровля мобильного здания является естественным молниеприемником, заменяющим стержневой молниеотвод.

Конструкция мобильного здания обеспечивает выполнение всех требований ПУЭ и «Инструкции по устройству молниезащиты зданий, сооружений и промышленных коммуникаций» к устройству защиты от прямых ударов молнии.

Ведомость ссылочных и прилагаемых документов

Обозначение	Наименование	Примечание
СП 29.13330.2011	Полы	
СП 16.13330.2017	Стальные конструкции	
СП 64.13330.2017	Деревянные конструкции	
СП 22.13330.2016	Основания зданий и сооружений	
СП 20.13330.2016	Нагрузки и воздействия	
СП 70.13330.2012	Несущие и ограждающие конструкции	
СП 28.13330.2017	Защита строительных конструкций от коррозии	
СП 131.13330.2020	Строительная климатология	
ГОСТ 30970-2014	Блоки дверные из поливинилхлоридных профилей	
ГОСТ 31173-2016	Блоки дверные стальные	
ГОСТ 30674-99	Блоки оконные из поливинилхлоридных профилей	

Ведомость рабочих чертежей основного комплекта

Ведомость рабочих чертежей основного комплек		
Лист №	Наименование	Примечание
1	Общие данные	
2	Общий вид	
3	Фасад	
4	Разрез	
5	Ведомость отделки помещений	
6	Схема расстановки дорожных плит	
7	Схема расстановки подрамников	
8	Схема расстановки БК	
9	Схема расстановки ферм и прогонов	
10	План кровли	
11	Схема укладки греющего кабеля	
12	План на отметке 0,000	
13	Схема расстановки оборудования	
14	Спецификация оборудования	
15	Схема расстановки сэндвич-панелей	
16	Спецификация	

Настоящий проект выполнен в соответствии с действующими нормами, правилами и стандартами, в том числе и по взрыво- и пожаробезопасности.


Главный инженер проекта (Скасырских Е.А.)

						02-26 МЗ-УТЦ АР			
						Здание мобильное МЗ-22 30100x27100x10180			
Изм.	Кол.уч.	Лист	№ док.	Подп.	Дата	Учебно-тренинговый центр	Стадия	Лист	Листов
Разработал		Терюшов О.В.			02.26			1	
Проверил		Скасырских Е.А.				Общие данные	ООО "ТЕХНОВЕКТОР"		
Утвердил		Хамурык А.В.							



RAL 9010
Стены наружные

RAL 7024
Крыша
Кровля входных групп
Входные группы
Цоколь (фасонные изделия)
Входные двери
Фасонные изделия над/под окнами
Фасонные изделия входных групп
Лестница на крышу с площадками
Наружный профиль окон
Отливы, откосы окон
Откосы входных дверей
Снегозадержатели
Водосток

Общий вид

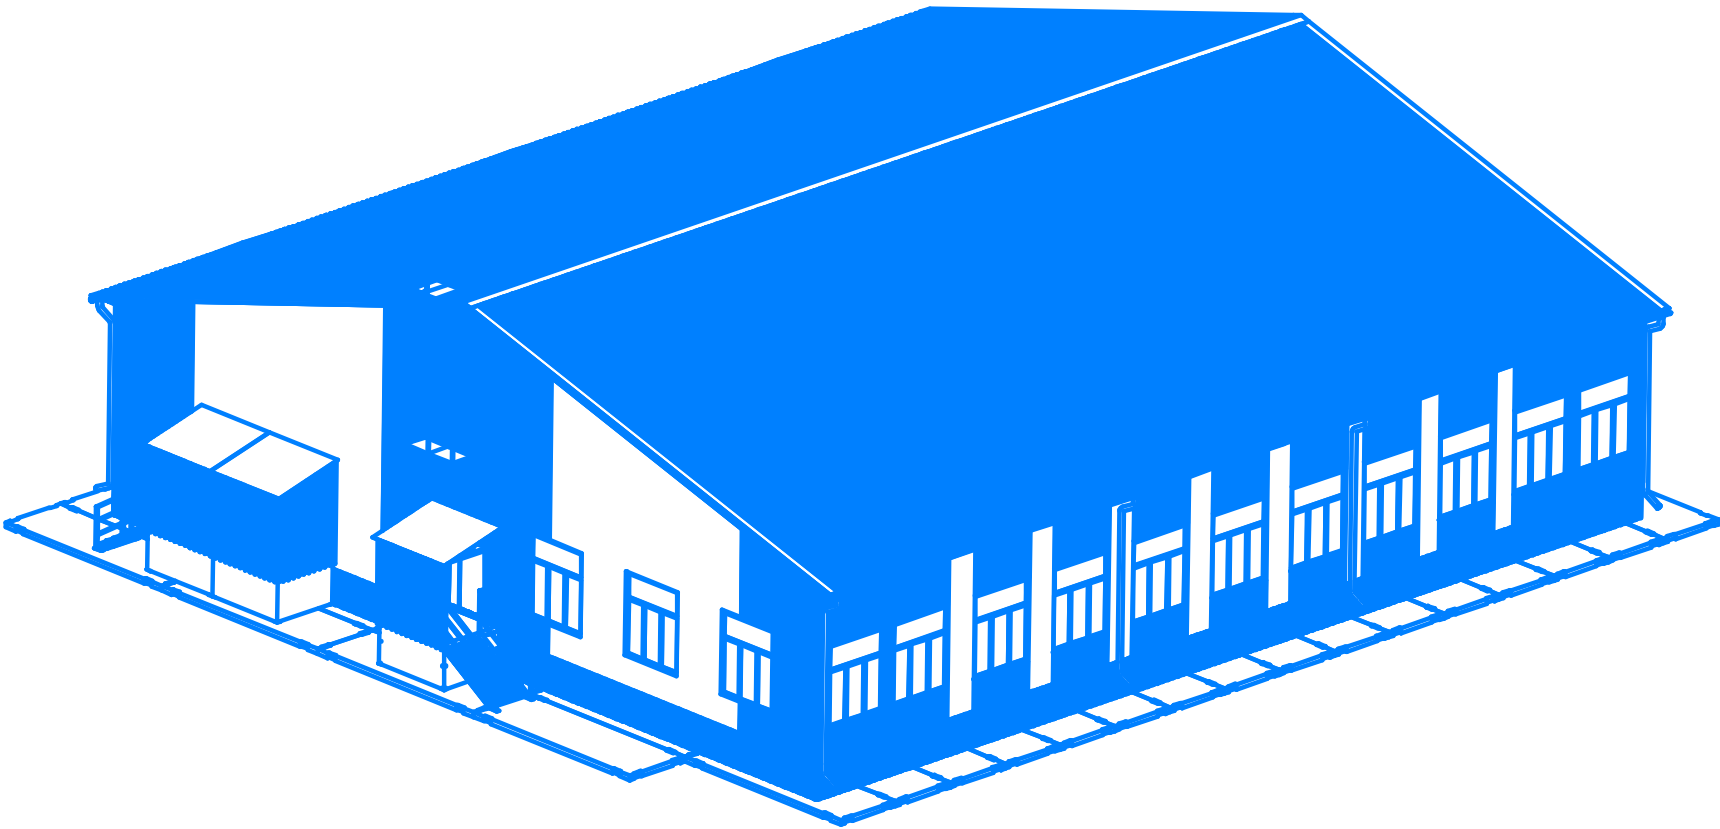

Входная группа центральная
Цоколь крыльца отделать профилированным листом С8 (RAL 7024)
Рейки выполнить из металла
Ступени и площадку крыльца отделать керамогранитом
плитка противоскользящая цвет серый

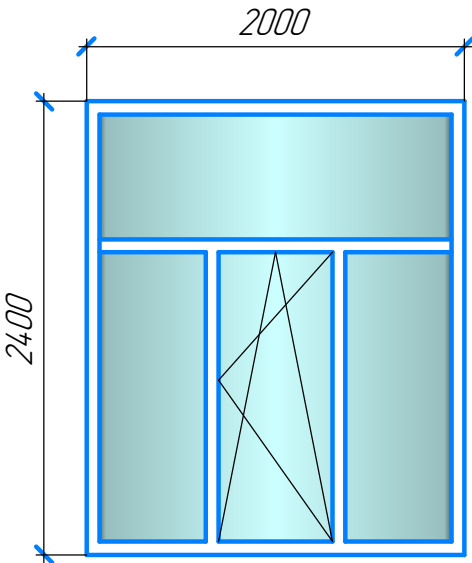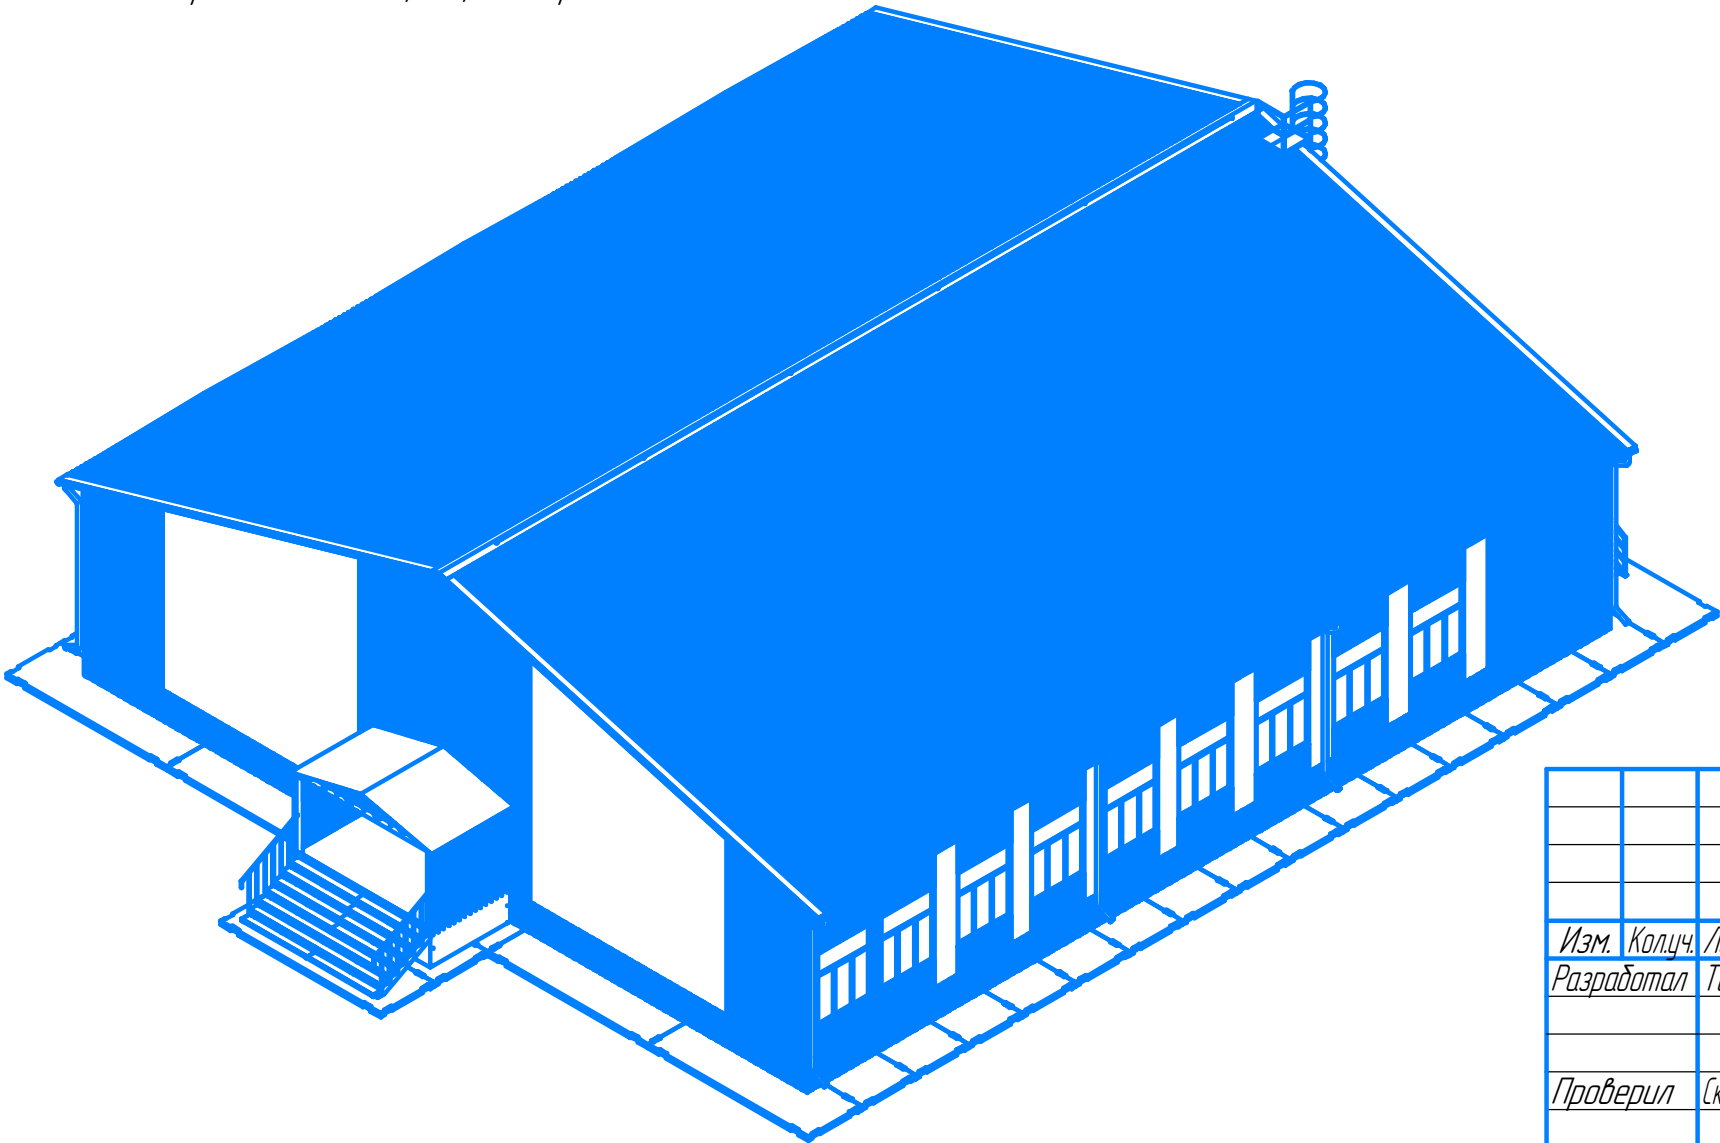

Согласовано	
Взам. инв. №	
Подп. и дата	
Инв. № подл.	

						02-26 МЗ-УТЦ АР		
						Здание мобильное МЗ-22 30100x27100x10180		
Изм.	Кол.ч.	Лист	№ док.	Подп.	Дата	Учебно-тренинговый центр	Стадия	Лист
Разработал		Терюшов О.В.			02.26			2
Проверил		Скасырских Е.А.				Общий вид	ООО "ТЕХНОВЕКТОР"	
Утвердил		Хамуряк А.В.						





Согласовано

Взам. инв. №

Подп. и дата


Инв. № подл.

Фасад

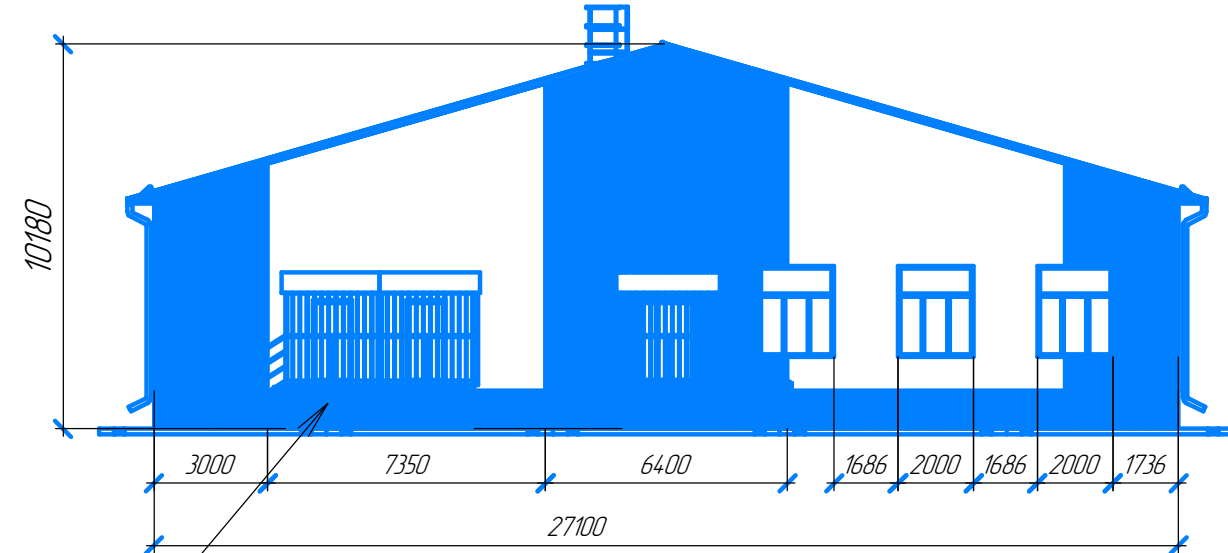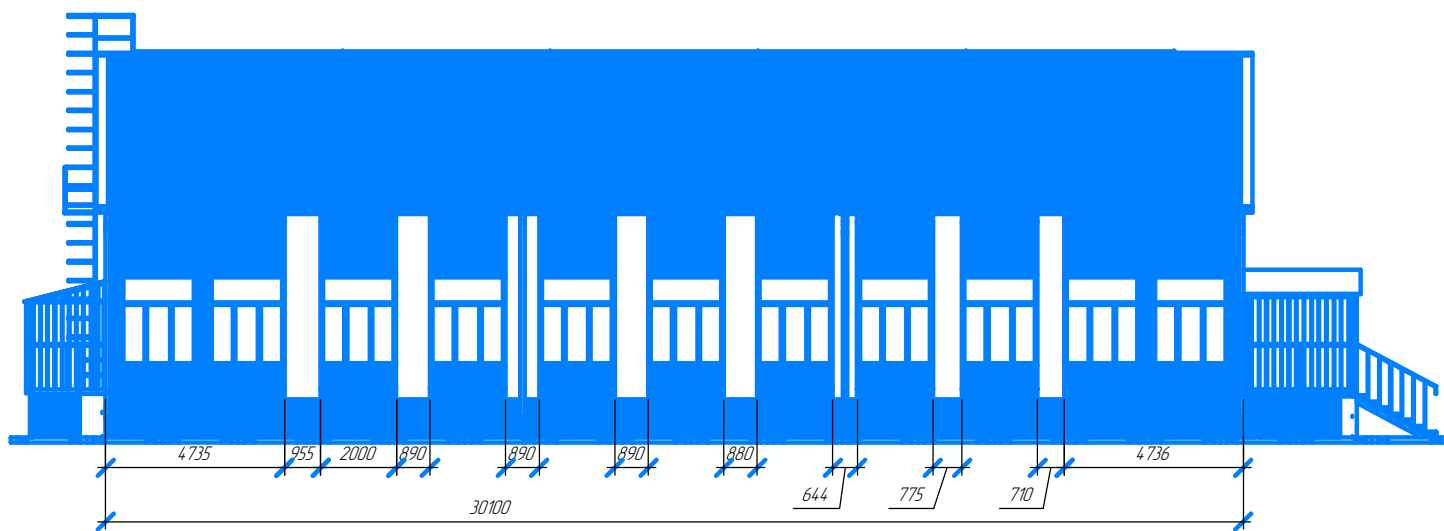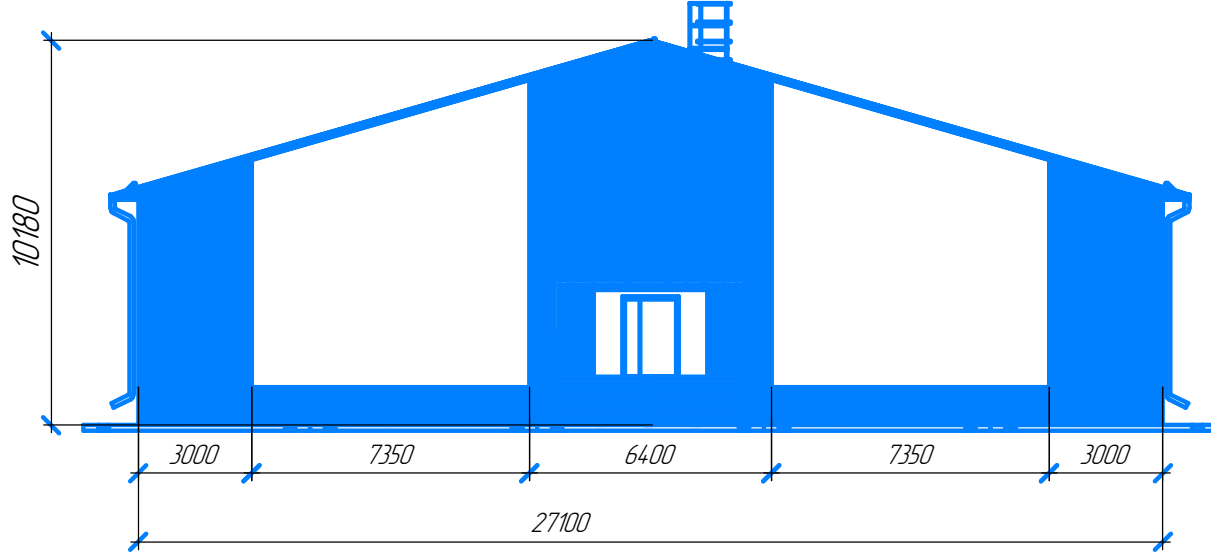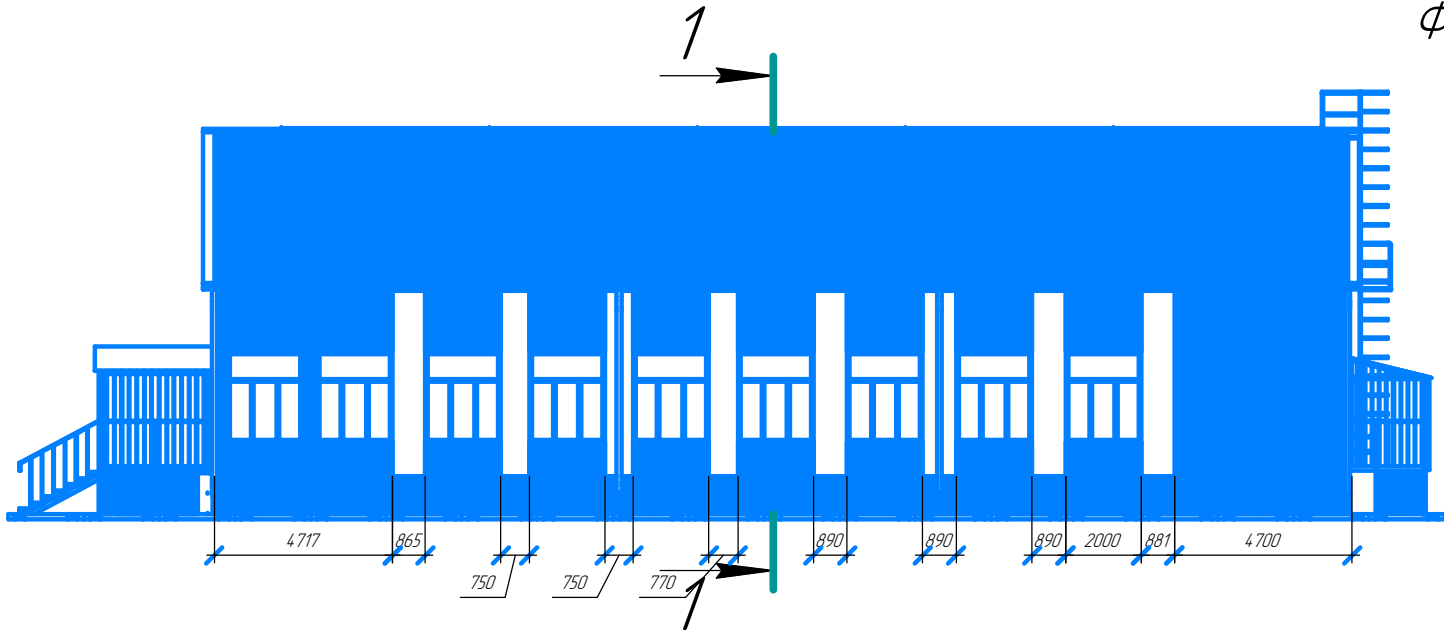


Входные группы обслуживания
Цоколь крыльца отделать профилированным листом С8 (RAL 7024)
Рейки выполнить из металла

Цветовое решение водосточных труб по фасаду
Водосточные трубы на сером серые на белом белые
Белые водосточные трубы окрасить в серый цвет
от границы фасонных изделий
закрывающих подрамники здания

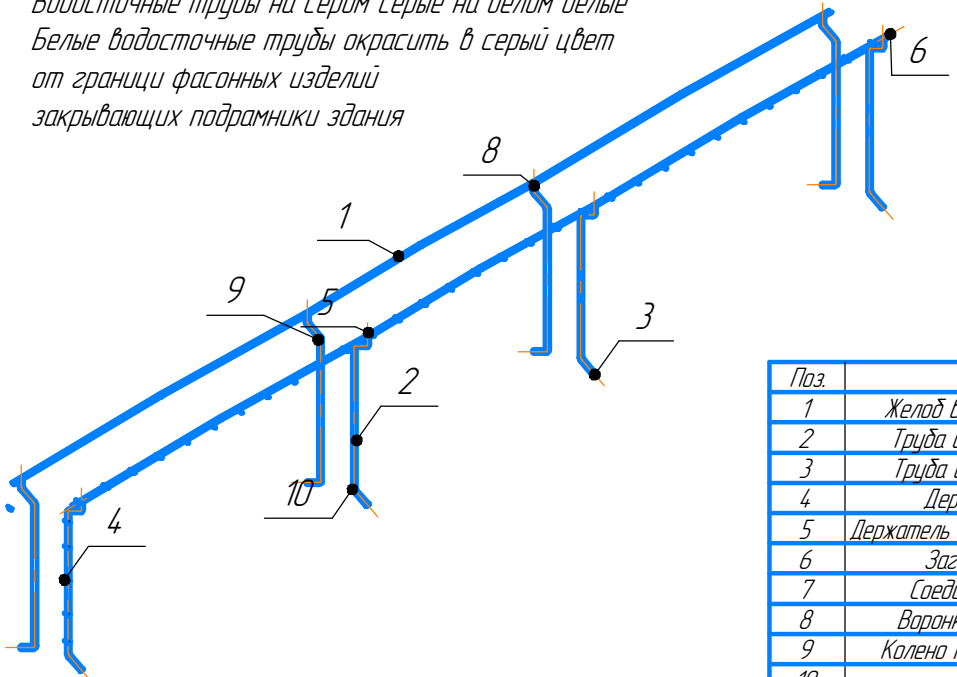


Поз.	Наименование	Кол.	Примечание
1	Желоб водосточный D125x3000	22	
2	Труба водосточная D90x3000	16	
3	Труба водосточная D90x1000	8	
4	Держатель трубы D90	40	
5	Держатель желоба карнизный D125x280	120	
6	Заглушка желоба D125	4	
7	Соединитель желоба D125	10	
8	Воронка выпускная D125/90	8	
9	Колена трубы D90x60 градусах	8	
10	Колена сливное	8	
11	Саморегулирующийся кабель	Расчет в разделе ЗОМ	

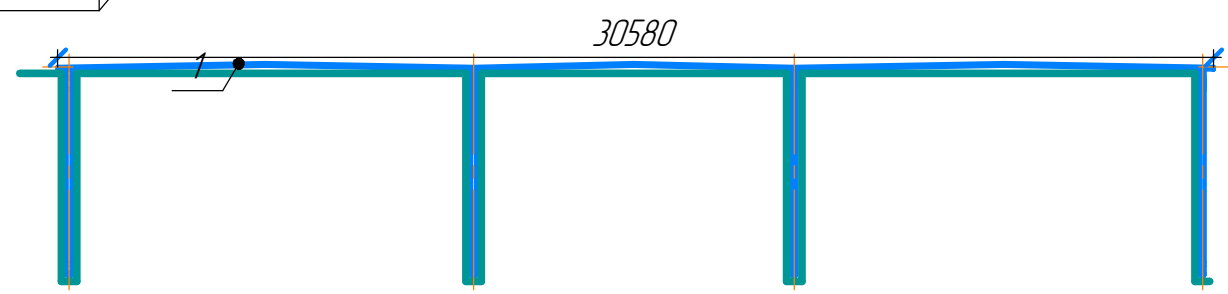


						02-26 МЗ-УТЦ АР			
						Здание мобильное МЗ-22 30100x27100x10180			
Изм.	Кол.уч.	Лист	№ док.	Подп.	Дата	Учебно-тренинговый центр	Стадия	Лист	Листов
Разработал		Терюшов О.В.			02.26			3	
Проверил		Скасырских Е.А.				Фасад	ООО "ТЕХНОВЕКТОР"		
Утвердил		Хамуряк А.В.							


Разрез

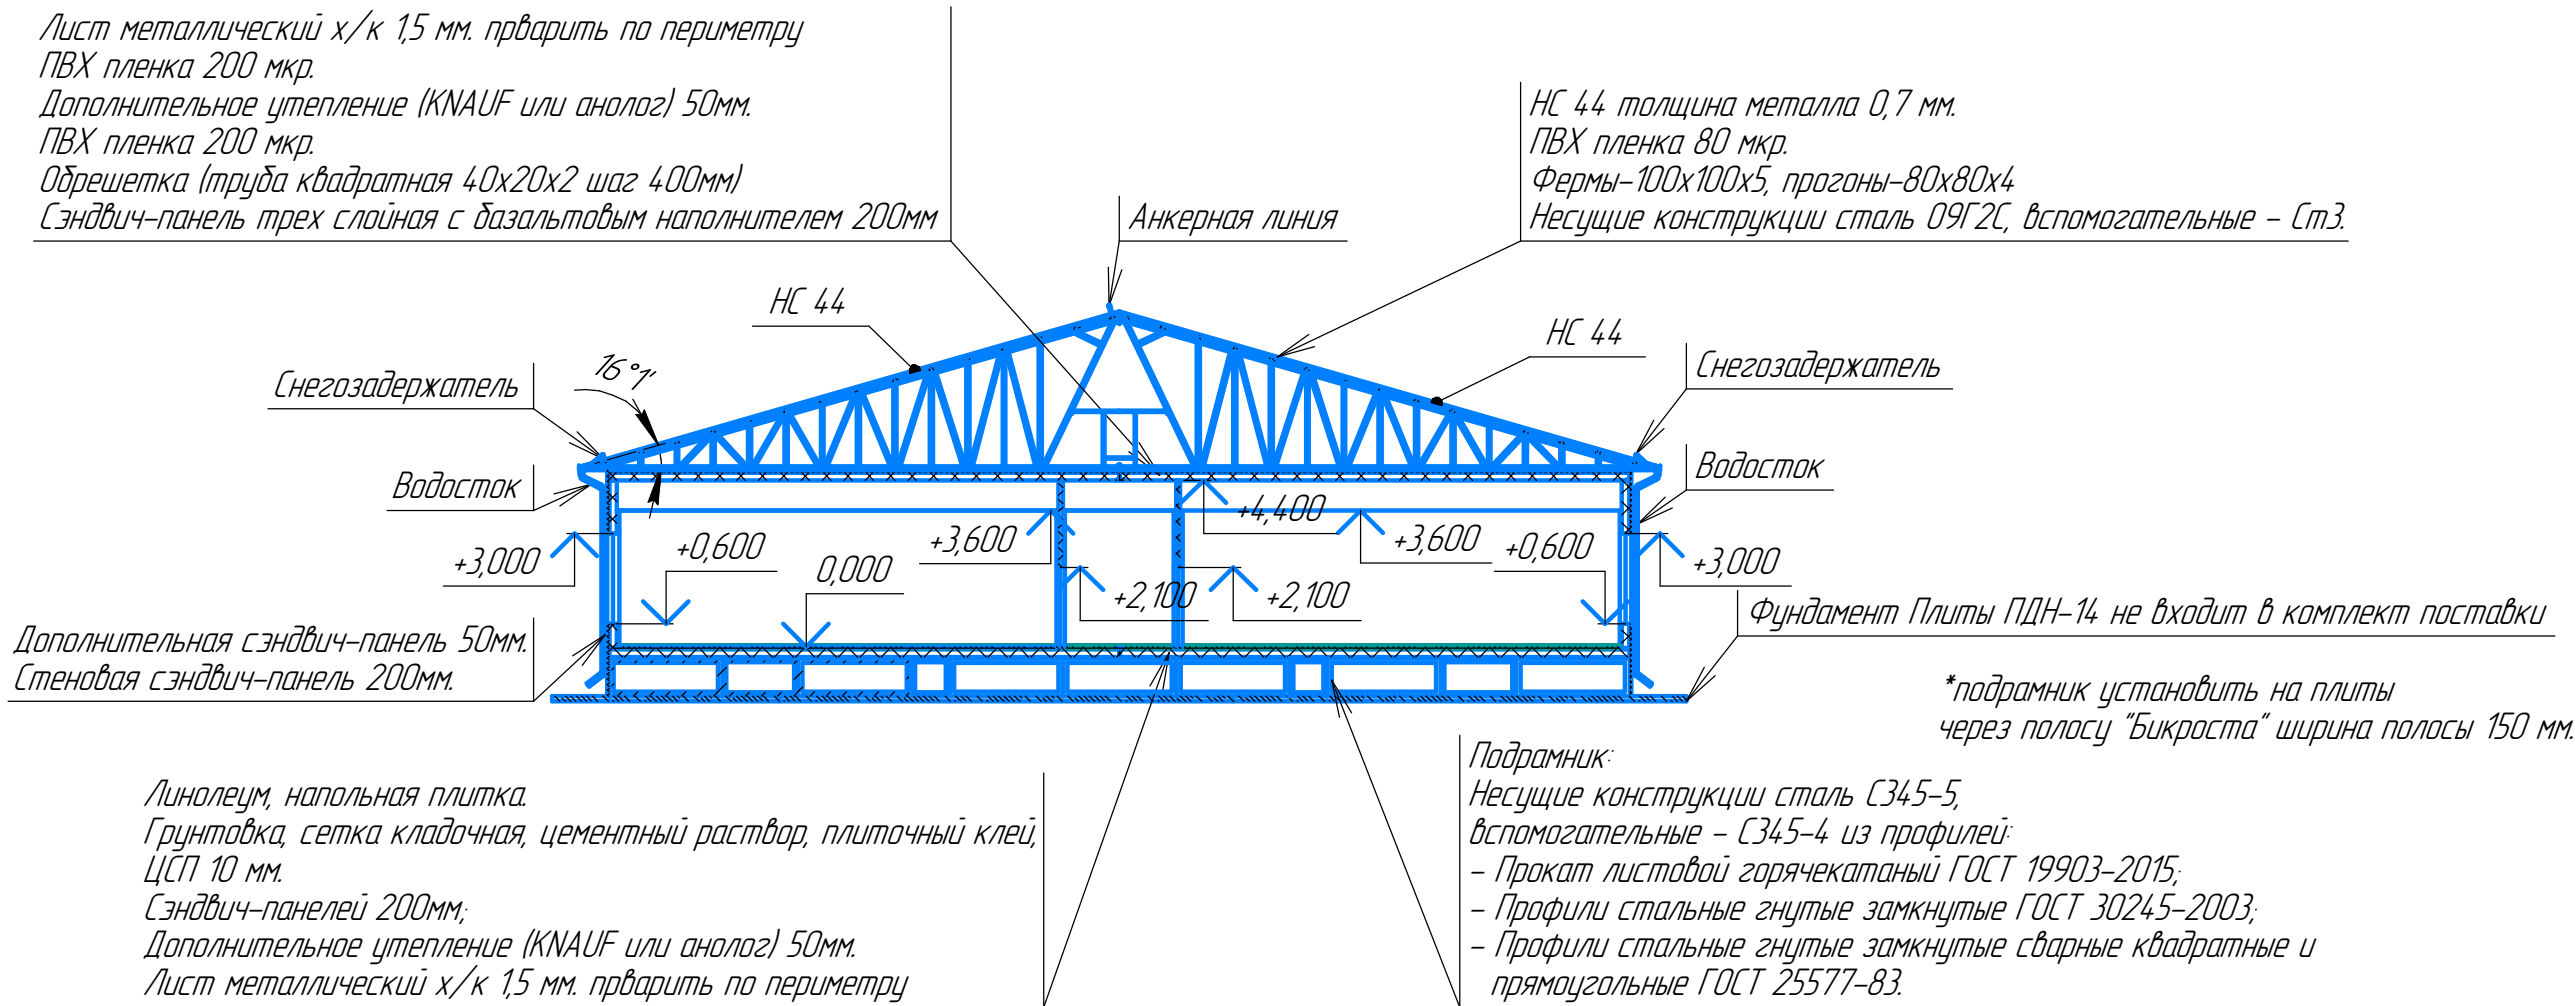


Узел стыковки перекрытия

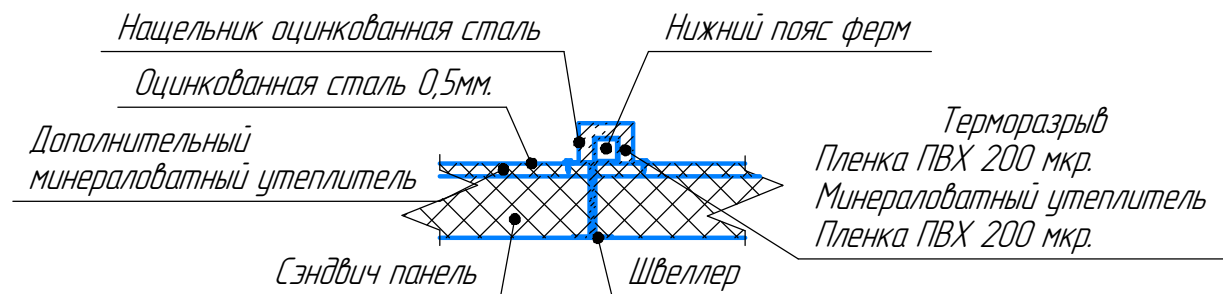

Узел стыковки БК низ

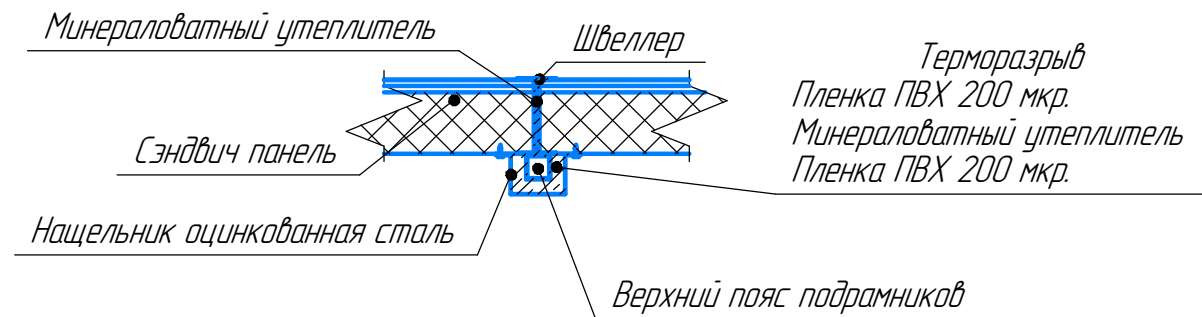

Узел стыковки стен

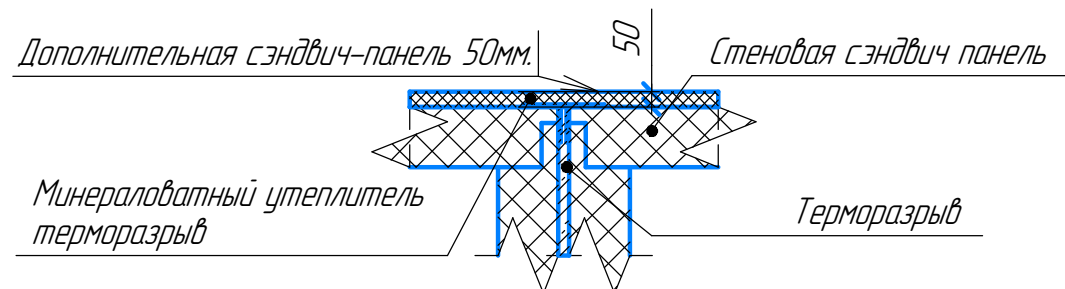

						02-26 МЗ-УТЦ АР		
						Здание мобильное МЗ-22 30100х27100х10180		
Изм.	Кол.уч.	Лист	№ док.	Подп.	Дата	Учебно-тренинговый центр	Стадия	Лист
Разработал	Терюшов О.В.				02.26			4
Проверил	Скасырских Е.А.					Разрез	ООО "ТЕХНОВЕКТОР"	
Утвердил	Хамурык А.В.							

Ведомость отделки помещений

Потолки.

- Учебные классы
- Гардероб
- Коридор
- Кабинеты преподавателей и спец. УТЦ
- Грильято потолок (стандарт) 75x75, H=40
- Толщина материала (мм): 0,4
- Размер решетки (мм): 600x600
- Материал: алюминий
- Цвет: белый матовый
- Санузел женский
- Санузел мужской
- Тех. помещение.
- Подвесной потолок. Поверхность белая ровная без перфорации.
- 100 % влагостойкий. Размер панелей (мм) 600x600.
- Серверная
- Электрощитовая
- ИТП
- Раздевалка
- Склад РВ
- Архив УТЦ
- Стеновыми сэндвич-панелями без дополнительной отделки цвет белый (RAL 9010).

Отделка стен:





- Учебные классы
- Кабинеты преподавателей и спец. УТЦ
- Гардероб
- Коридор
- Декоративные стеновые панели на основе ГКЛ (HPL пластик),
- толщина: 12,5 мм. плотность: 0,86 г/см3
- Класс пожарной опасности: КМ-1, цвет согласно дизайна
- Класс корп. обучения №1
- Раздвижная перегородка. Фиксация – Потолочный рельс
- Ширина панели – не менее 1500 мм.
- Толщина – 105 мм. Материал каркаса – алюминиевый
- Звукоизоляция – 45 дБ, цвет согласно дизайна
- Раздевалка
- Склад
- Архив
- Черновая обшивка стен ГКЛ листами к обрешетке с шагом 400 мм.
- Окраска водоземлемой краской, влагостойкой цвет серый (RAL 7035)
- Санузел женский
- Санузел мужской
- Тех. помещение
- Керамогранит, размер (600x600мм) цвет: белый «под мрамор» схема раскладки плитки: прямая.
- Керамическая плитка размер 20ммx80ммx9мм цвет: светло серый схема раскладки плитки: прямая.
- Окраска водоземлемой краской, влагостойкой, цвет белый (RAL 9010)
- Отделка керамической плиткой выполняется согласно дизайна

Напольное покрытие:

- Учебные классы
- Кабинеты преподавателей и спец. УТЦ
- Склад
- Гардероб
- Раздевалка
- Линолеум коммерческий гетерогенный антистатический,
- толщина 2мм, класс покрытия 34, класс пожарного сертификата КМ2;
- Плинтус напольный ударопрочный дюрополимер 80мм цвет серый (RAL 7024)
- Коридор
- Керамогранит, износостойкость PEI IV размер (мм) 600x600
- цвет: серый под бетон схема раскладки плитки: прямая.
- Гидроизоляция, плинтус напольный ударопрочный дюрополимер 80мм цвет серый (RAL 7024)
- Санузел женский
- Санузел мужской
- Тех. помещение
- Керамогранит, «под мрамор», белый, матовый, размер (мм) 600x600,
- износостойкость PEI IV; схема раскладки плитки: прямая
- Плинтус напольный ударопрочный дюрополимер 80мм цвет белый (RAL 9010)

						02-26 МЗ-УТЦ АР		
						Здание мобильное МЗ-22		
						30100x27100x10180		
Изм.	Кол.уч.	Лист	№ док.	Подп.	Дата	Учебно-тренинговый центр	Стадия	Лист
Разработал	Терюшов О.В.				02.26			5
Проверил	Скасырских Е.А.					Ведомость отделки помещений	ООО "ТЕХНОВЕКТОР"	
Утвердил	Хамуряк А.В.							

Схема расстановки дорожных плит (86 шт.)

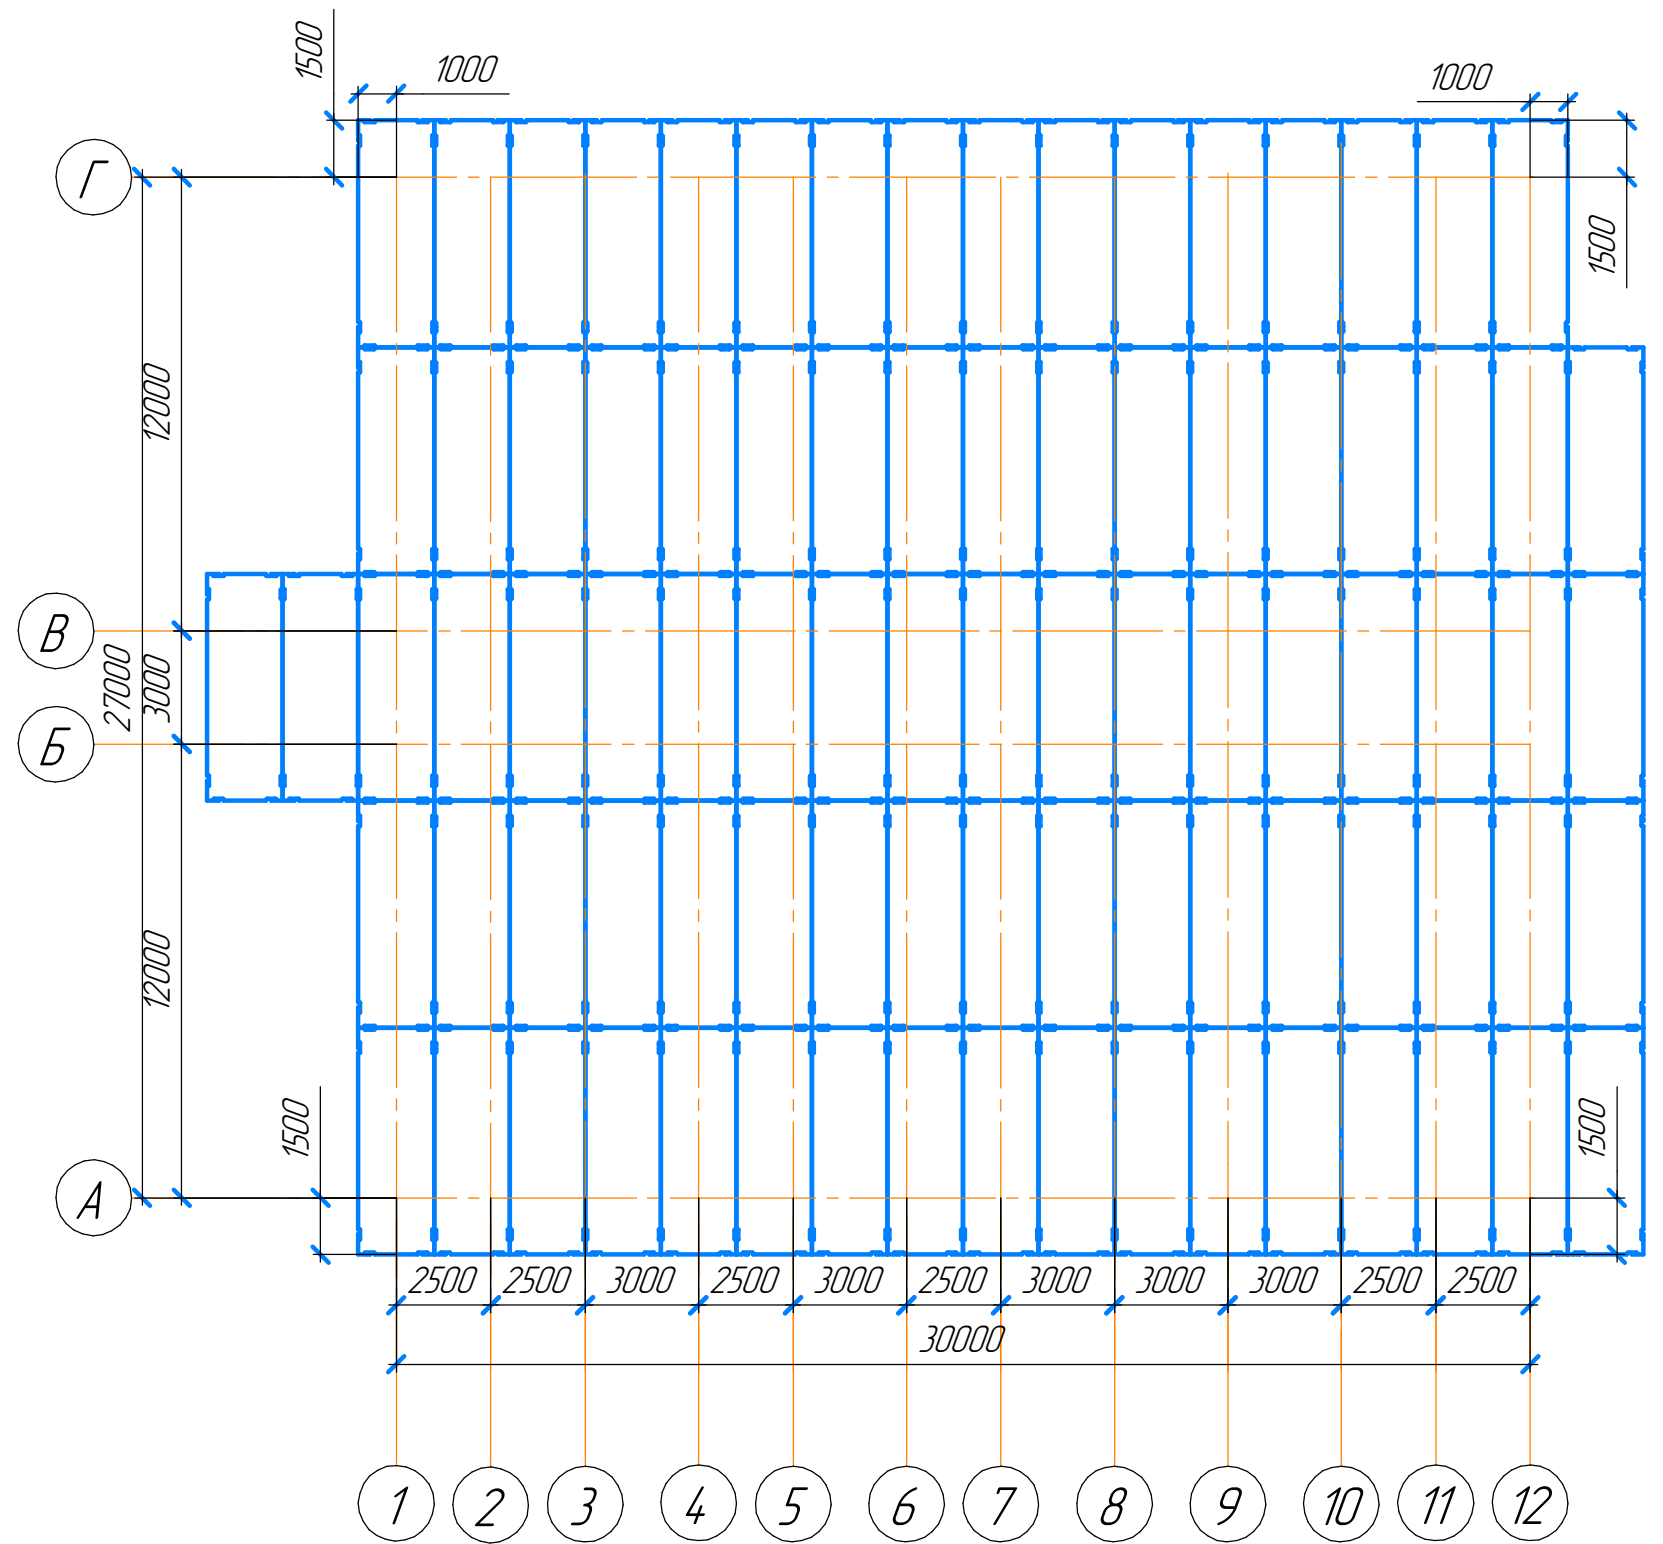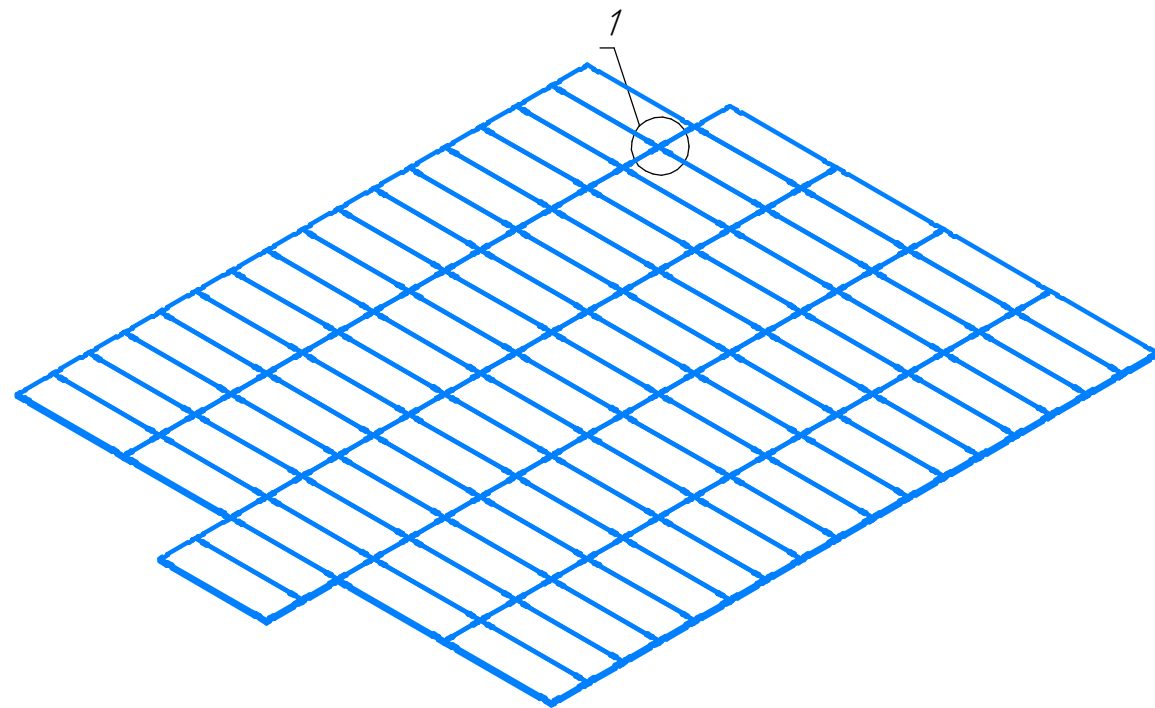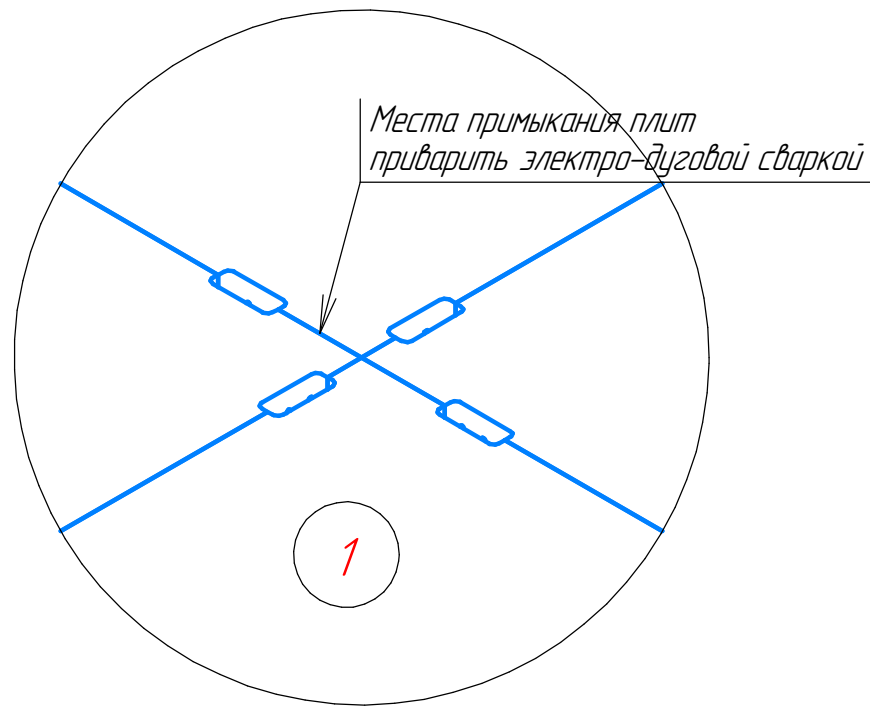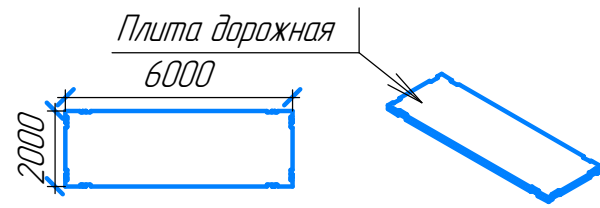

						02-26 МЗ-УТЦ АР		
						Здание мобильное МЗ-22 30100x27100x10180		
Изм.	Колуч.	Лист	№ док.	Подп.	Дата	Учебно-тренинговый центр	Стандия	Лист
Разработал	Терюшов О.В.				02.26			6
Проверил	Скасырских Е.А.					Схема расстановки дорожных плит	ООО "ТЕХНОВЕКТОР"	
Утвердил	Хамуряк А.В.							

Формат А3

Согласовано

ВЗАМ. УНВ. №


Подн. и дама

ИНВ. № подл.





Схема расстановки подрамников

Обоз.	Наименование	Размер	Кол.шт.
Пд1	Подрамник	16000х3000х1000	6
Пд2	Подрамник	14000х3000х1000	6
Св1	Связь	2000х1000	2
Св2	Связь	200х1000	2
Св3	Связь	2000х1000	2
Св4	Связь	1000х1000	6
Св5	Связь	3000х1000	6

*связи к подрамникам закрепить с помощью электро-дуговой сварки

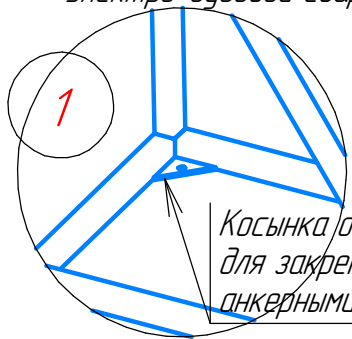

Косынка опорная t=10 мм. (6 шт.)
для закрепления подрамников к плитам
анкерными болтами d 20мм.

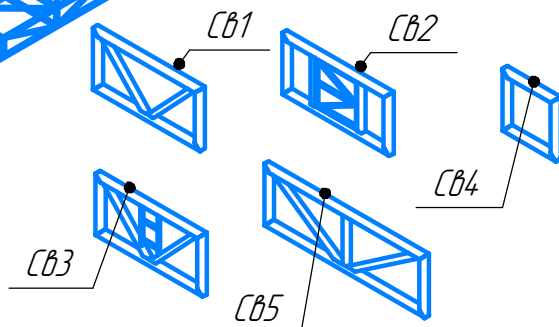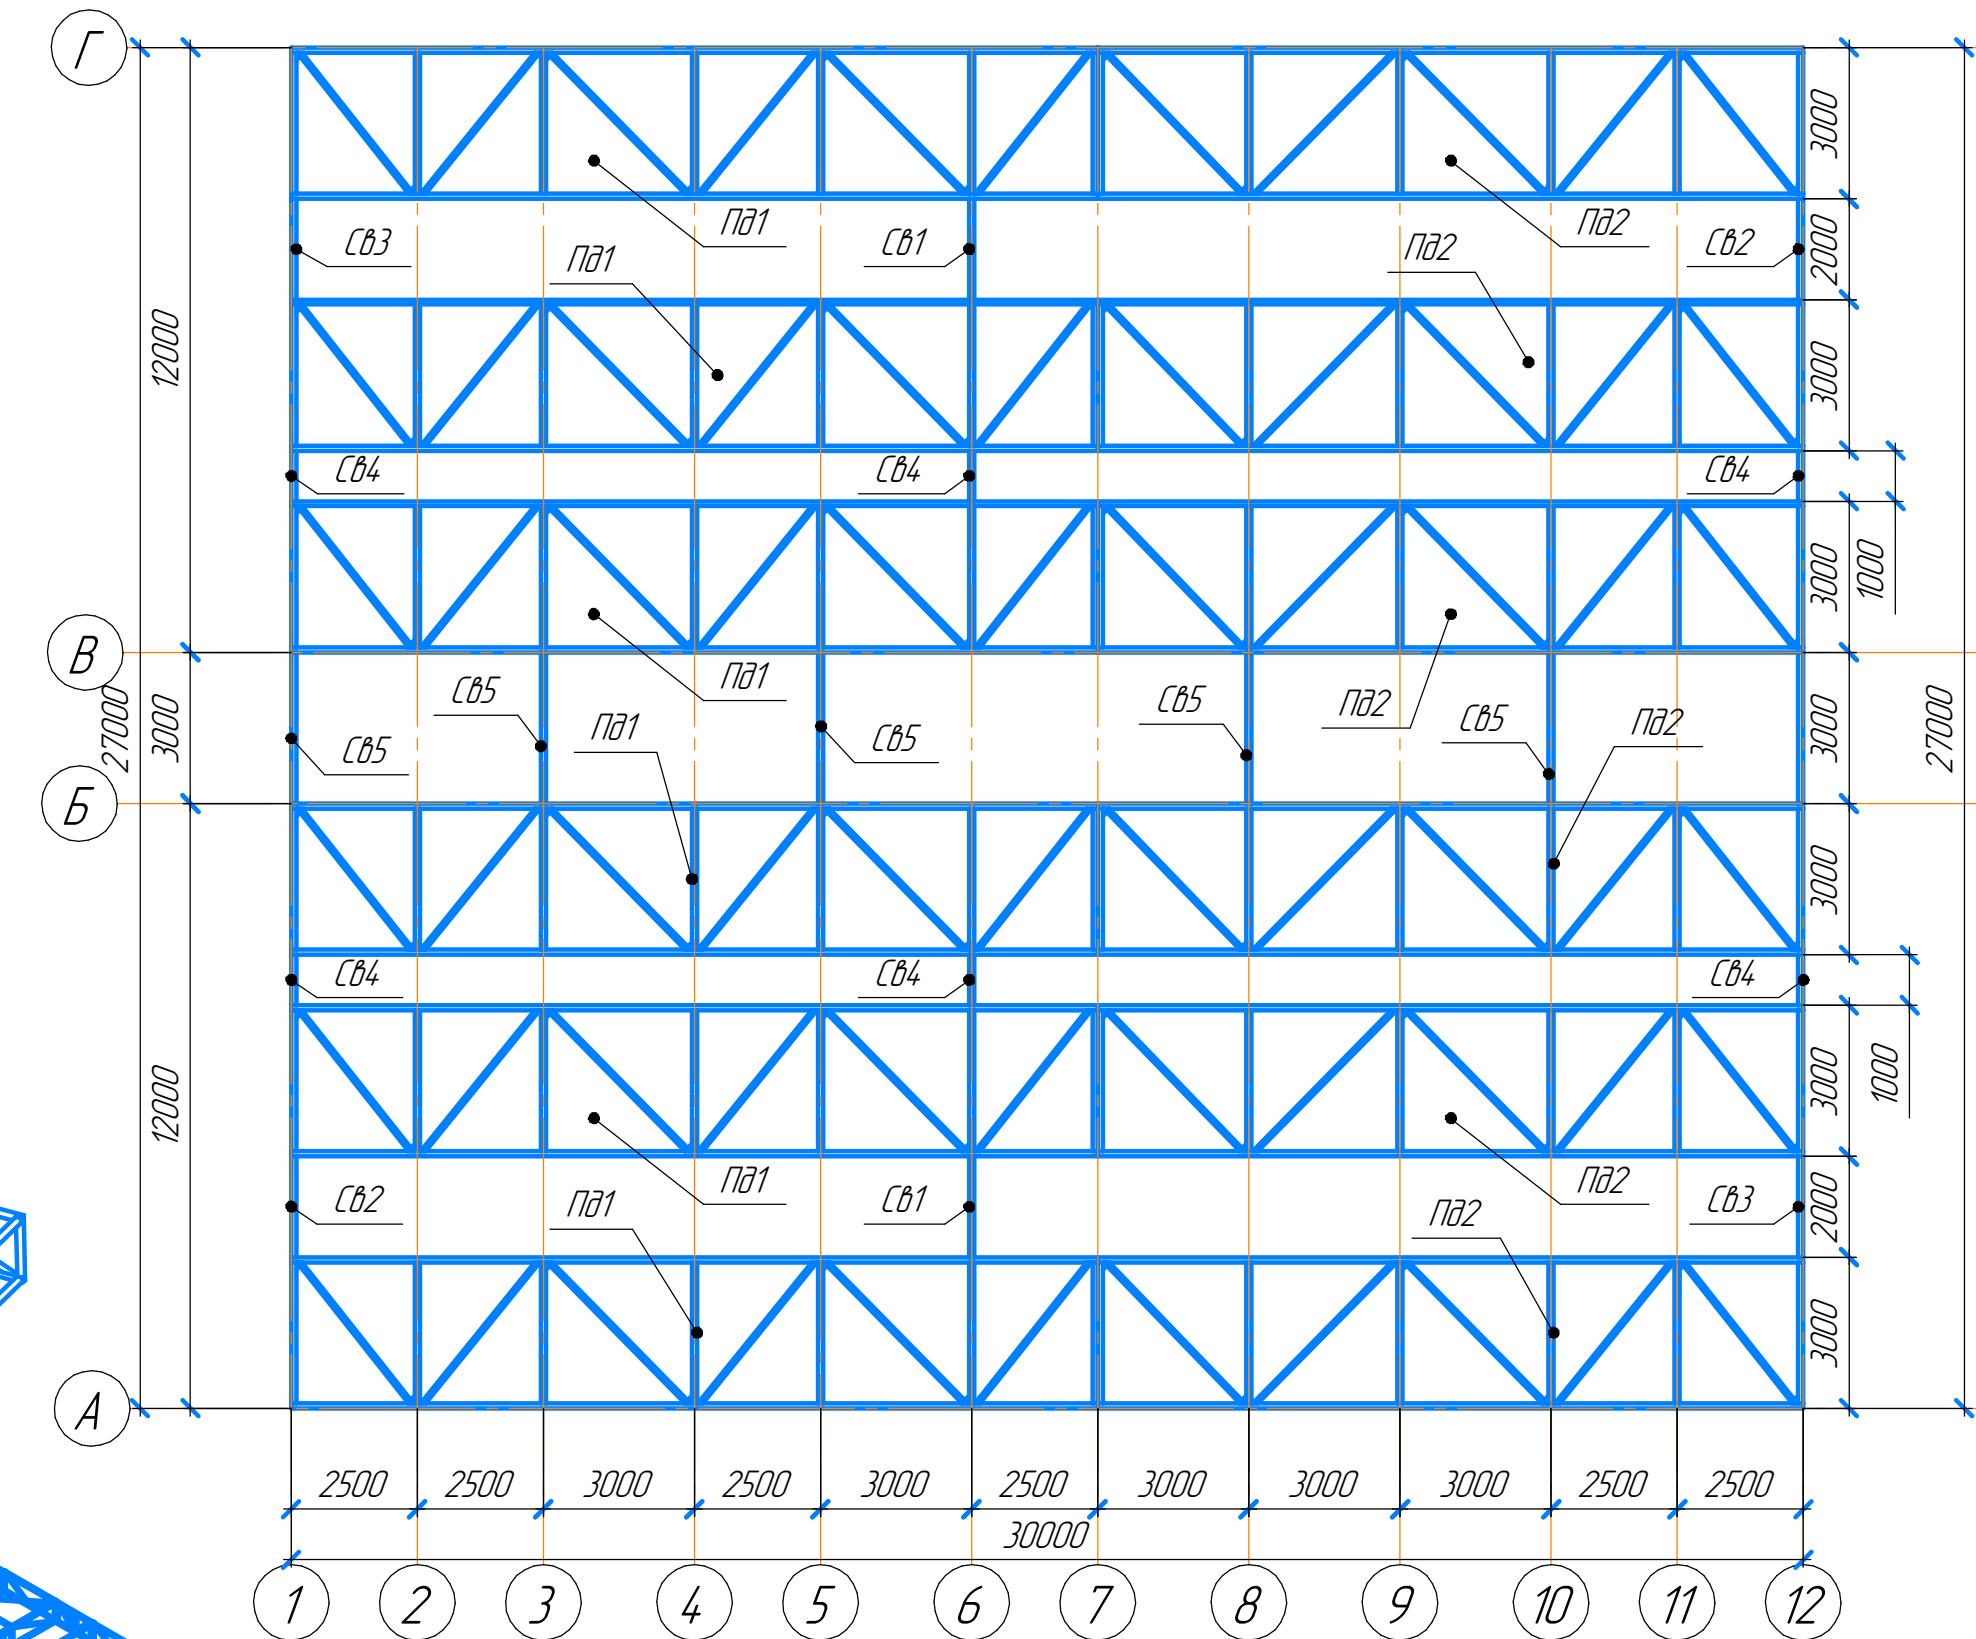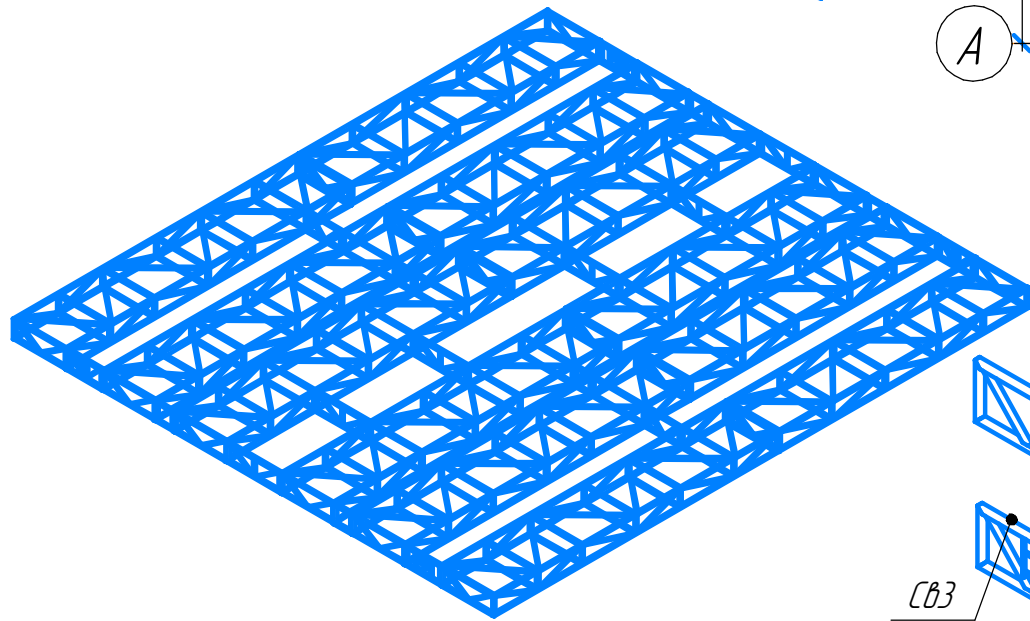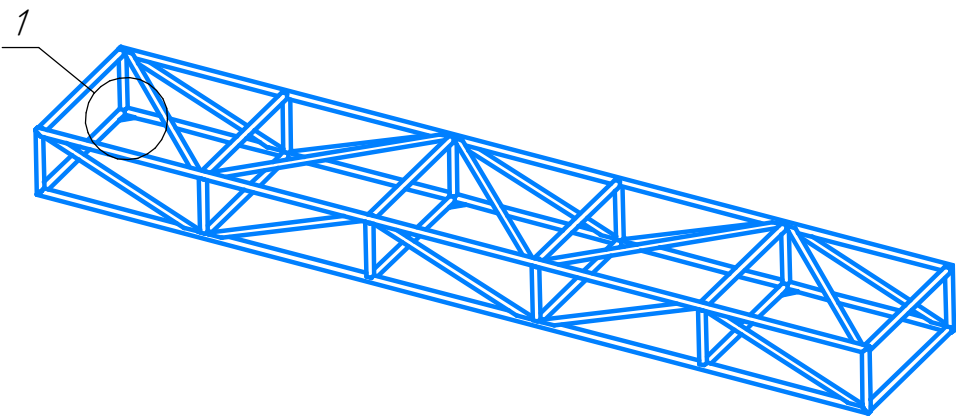

02-26 МЗ-УТЦ АР					
Здание мобильное МЗ-22 30100х27100х10180					
Изм.	Кол.уч.	Лист	№ док.	Подп.	Дата
Разработал	Терюшов О.В.				02.26
Проверил	Скасырских Е.А.				
Утвердил	Хамуряк А.В.				
Учебно-тренинговый центр				Стadia	Лист
Схема расстановки подрамников				7	Листов
ООО "ТЕХНОВЕКТОР"					

Верхнее крыло Блок контейнеров


Обоз.	Наименование	Размер	К-во шт.	Примечание
БК1	Блок-контейнер	13500x2500x4 975	1	
БК2	Блок-контейнер	13500x2500x4 975	1	
БК3	Блок-контейнер	13500x3000x4 975	1	
БК4	Блок-контейнер	13500x2500x4 975	1	
БК5	Блок-контейнер	13500x3000x4 975	1	
БК6	Блок-контейнер	13500x2500x4 975	1	
БК7	Блок-контейнер	13500x3000x4 975	1	
БК8	Блок-контейнер	13500x3000x4 975	1	
БК9	Блок-контейнер	13500x3000x4 975	1	
БК10	Блок-контейнер	13500x2500x4 975	1	
БК11	Блок-контейнер	13500x2500x4 975	1	

Нижнее крыло Блок контейнеров

Обоз.	Наименование	Размер	К-во шт.	Примечание
БК12	Блок-контейнер	13500x2500x4 975	1	
БК13	Блок-контейнер	13500x2500x4 975	1	
БК14	Блок-контейнер	13500x1400x4 975	1	
БК15	Блок-контейнер	13500x2500x4 975	1	
БК16	Блок-контейнер	13500x3000x4 975	1	
БК17	Блок-контейнер	13500x2500x4 975	1	
БК18	Блок-контейнер	13500x3000x4 975	1	
БК19	Блок-контейнер	13500x3000x4 975	1	
БК20	Блок-контейнер	13500x3000x4 975	1	
БК21	Блок-контейнер	13500x2500x4 975	1	
БК22	Блок-контейнер	13500x2500x4 975	1	

Обоз.	Наименование	Сечение	К-во шт.	Примечание
УСт1	Угловая стойка блока	125x125x8	44	
УСт2	Угловая стойка блока	100x100x8	44	
Ст1	Стойка внутри стен	60x60x4	20	
Ст2	Стойка внутри стен	80x80x4	17	
СВК	Связь крестовая	60x60x4	30	

Схема расстановки блок-контейнеров, стоек и связей

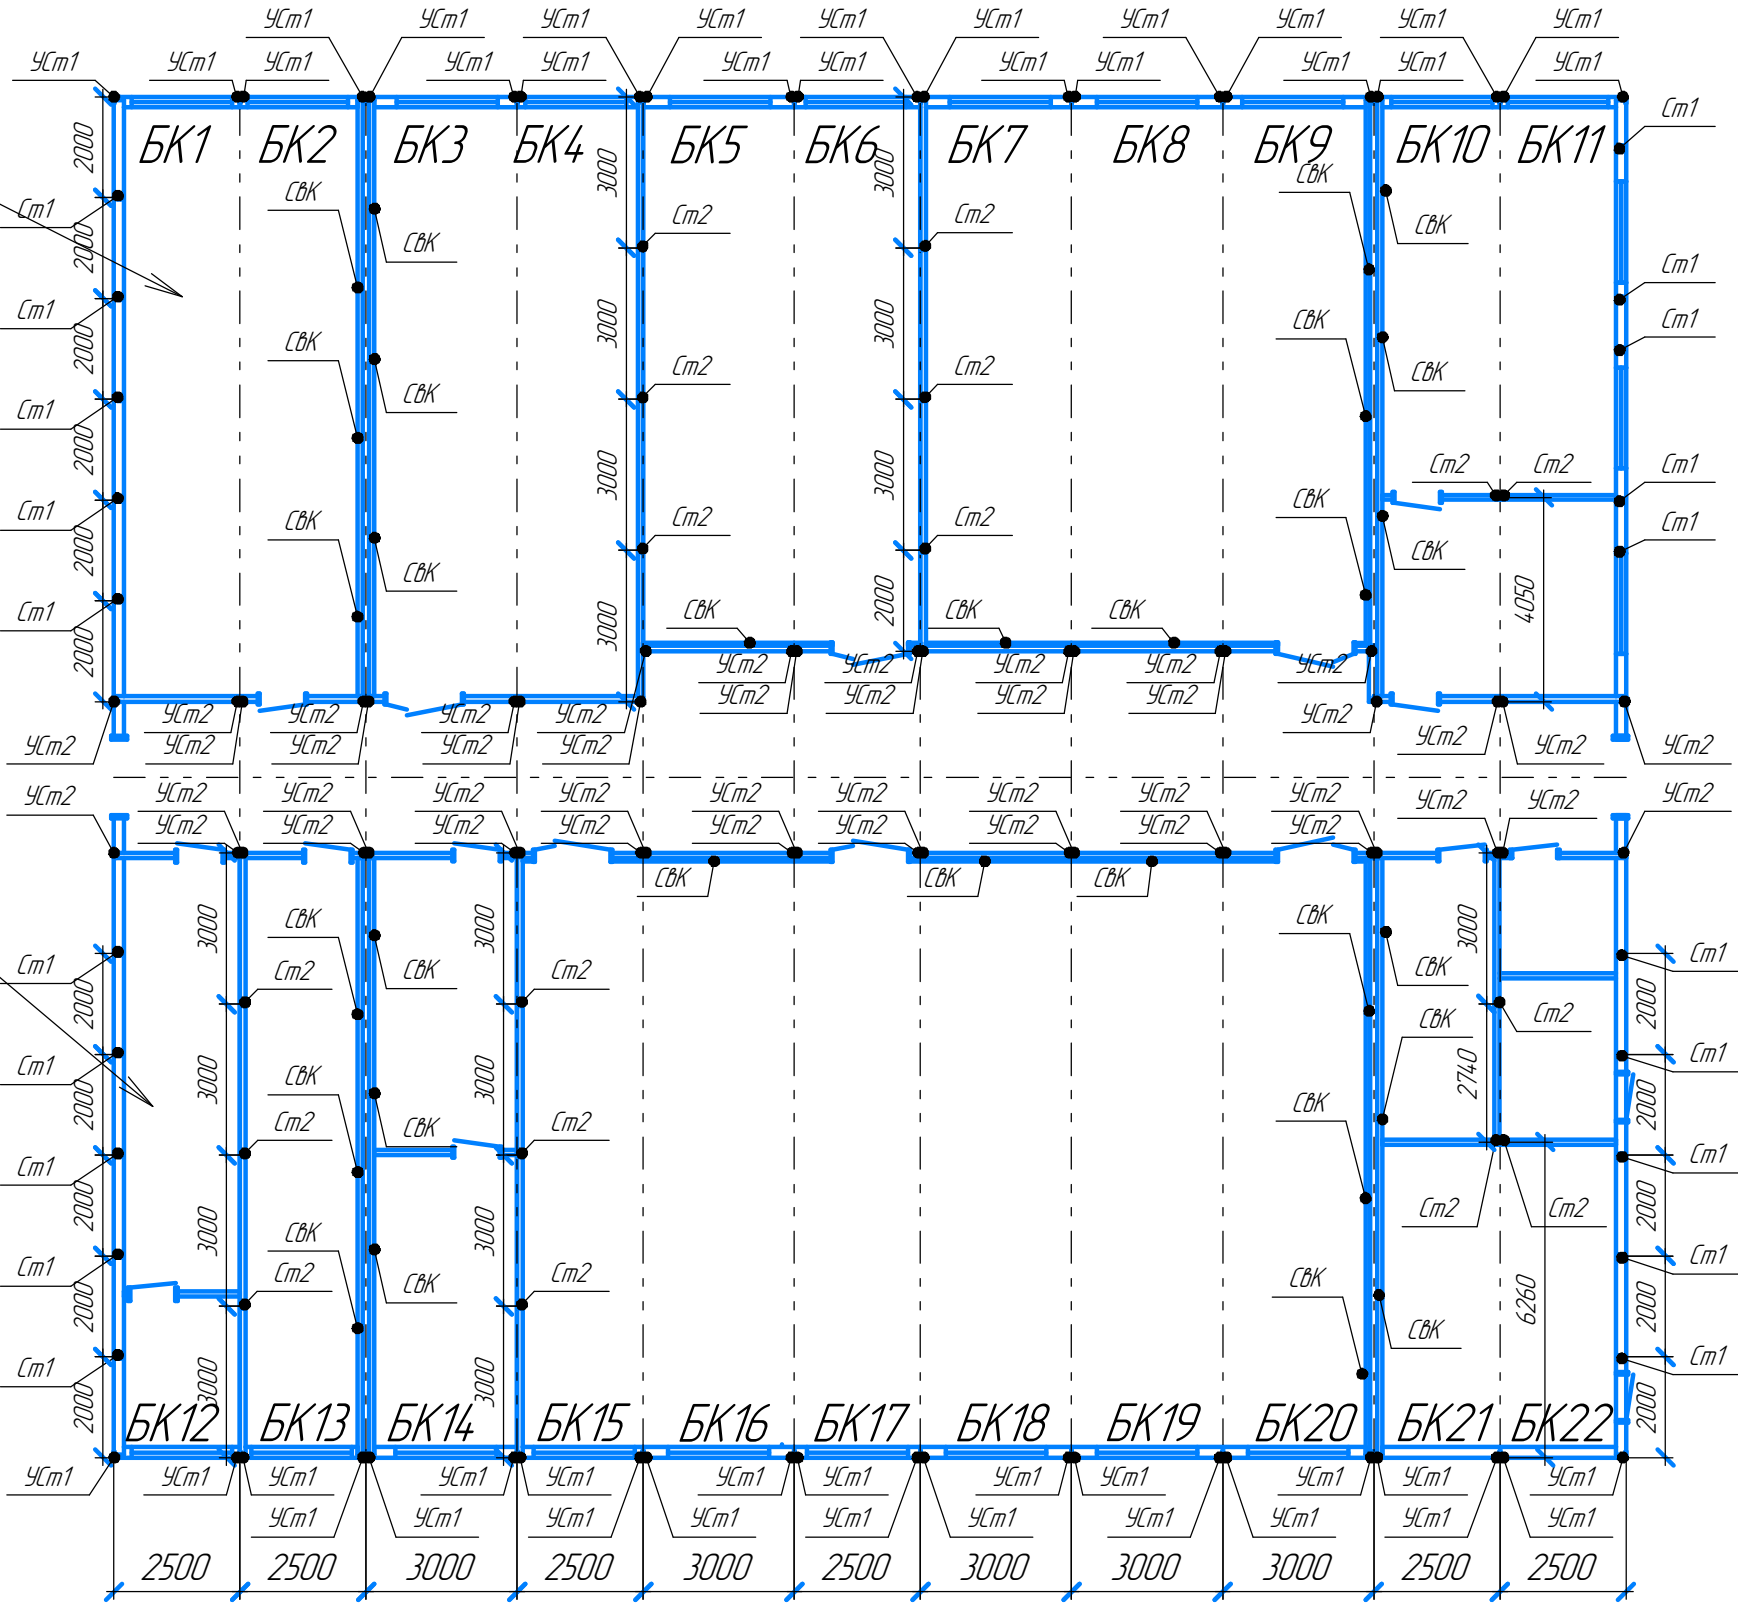

*блок-контейнера к подрамникам закрепить с помощью электро-дуговой сварки

02-26 МЗ-УТЦ АР

Здание мобильное МЗ-22
30100x27100x10180

Изм.	Кол.уч.	Лист	№ док.	Подп.	Дата
Разработал	Терюшов О.В.				02.26
Проверил	Скасырских Е.А.				
Утвердил	Хамуряк А.В.				

Учебно-тренинговый центр

Схема расстановки блок-контейнеров,
стоек и связей

Стadia	Лист	Листов
	8	


ООО "ТЕХНОВЕКТОР"

Формат А3

Схема расстановки ферм и прогонов

Обоз.	Наименование	Размер	Кол.шт.
ПФс1	Полу-Ферма	14150x4080	4
ПФс2	Полу-Ферма	14150x4080	20

Обоз.	Наименование	Сечение	Размер	Кол.шт.
Пр1	Прогон	80x80x4	13850	30
Пр2	Прогон	80x80x4	11500	30
Пр3	Прогон	80x80x4	5230	30

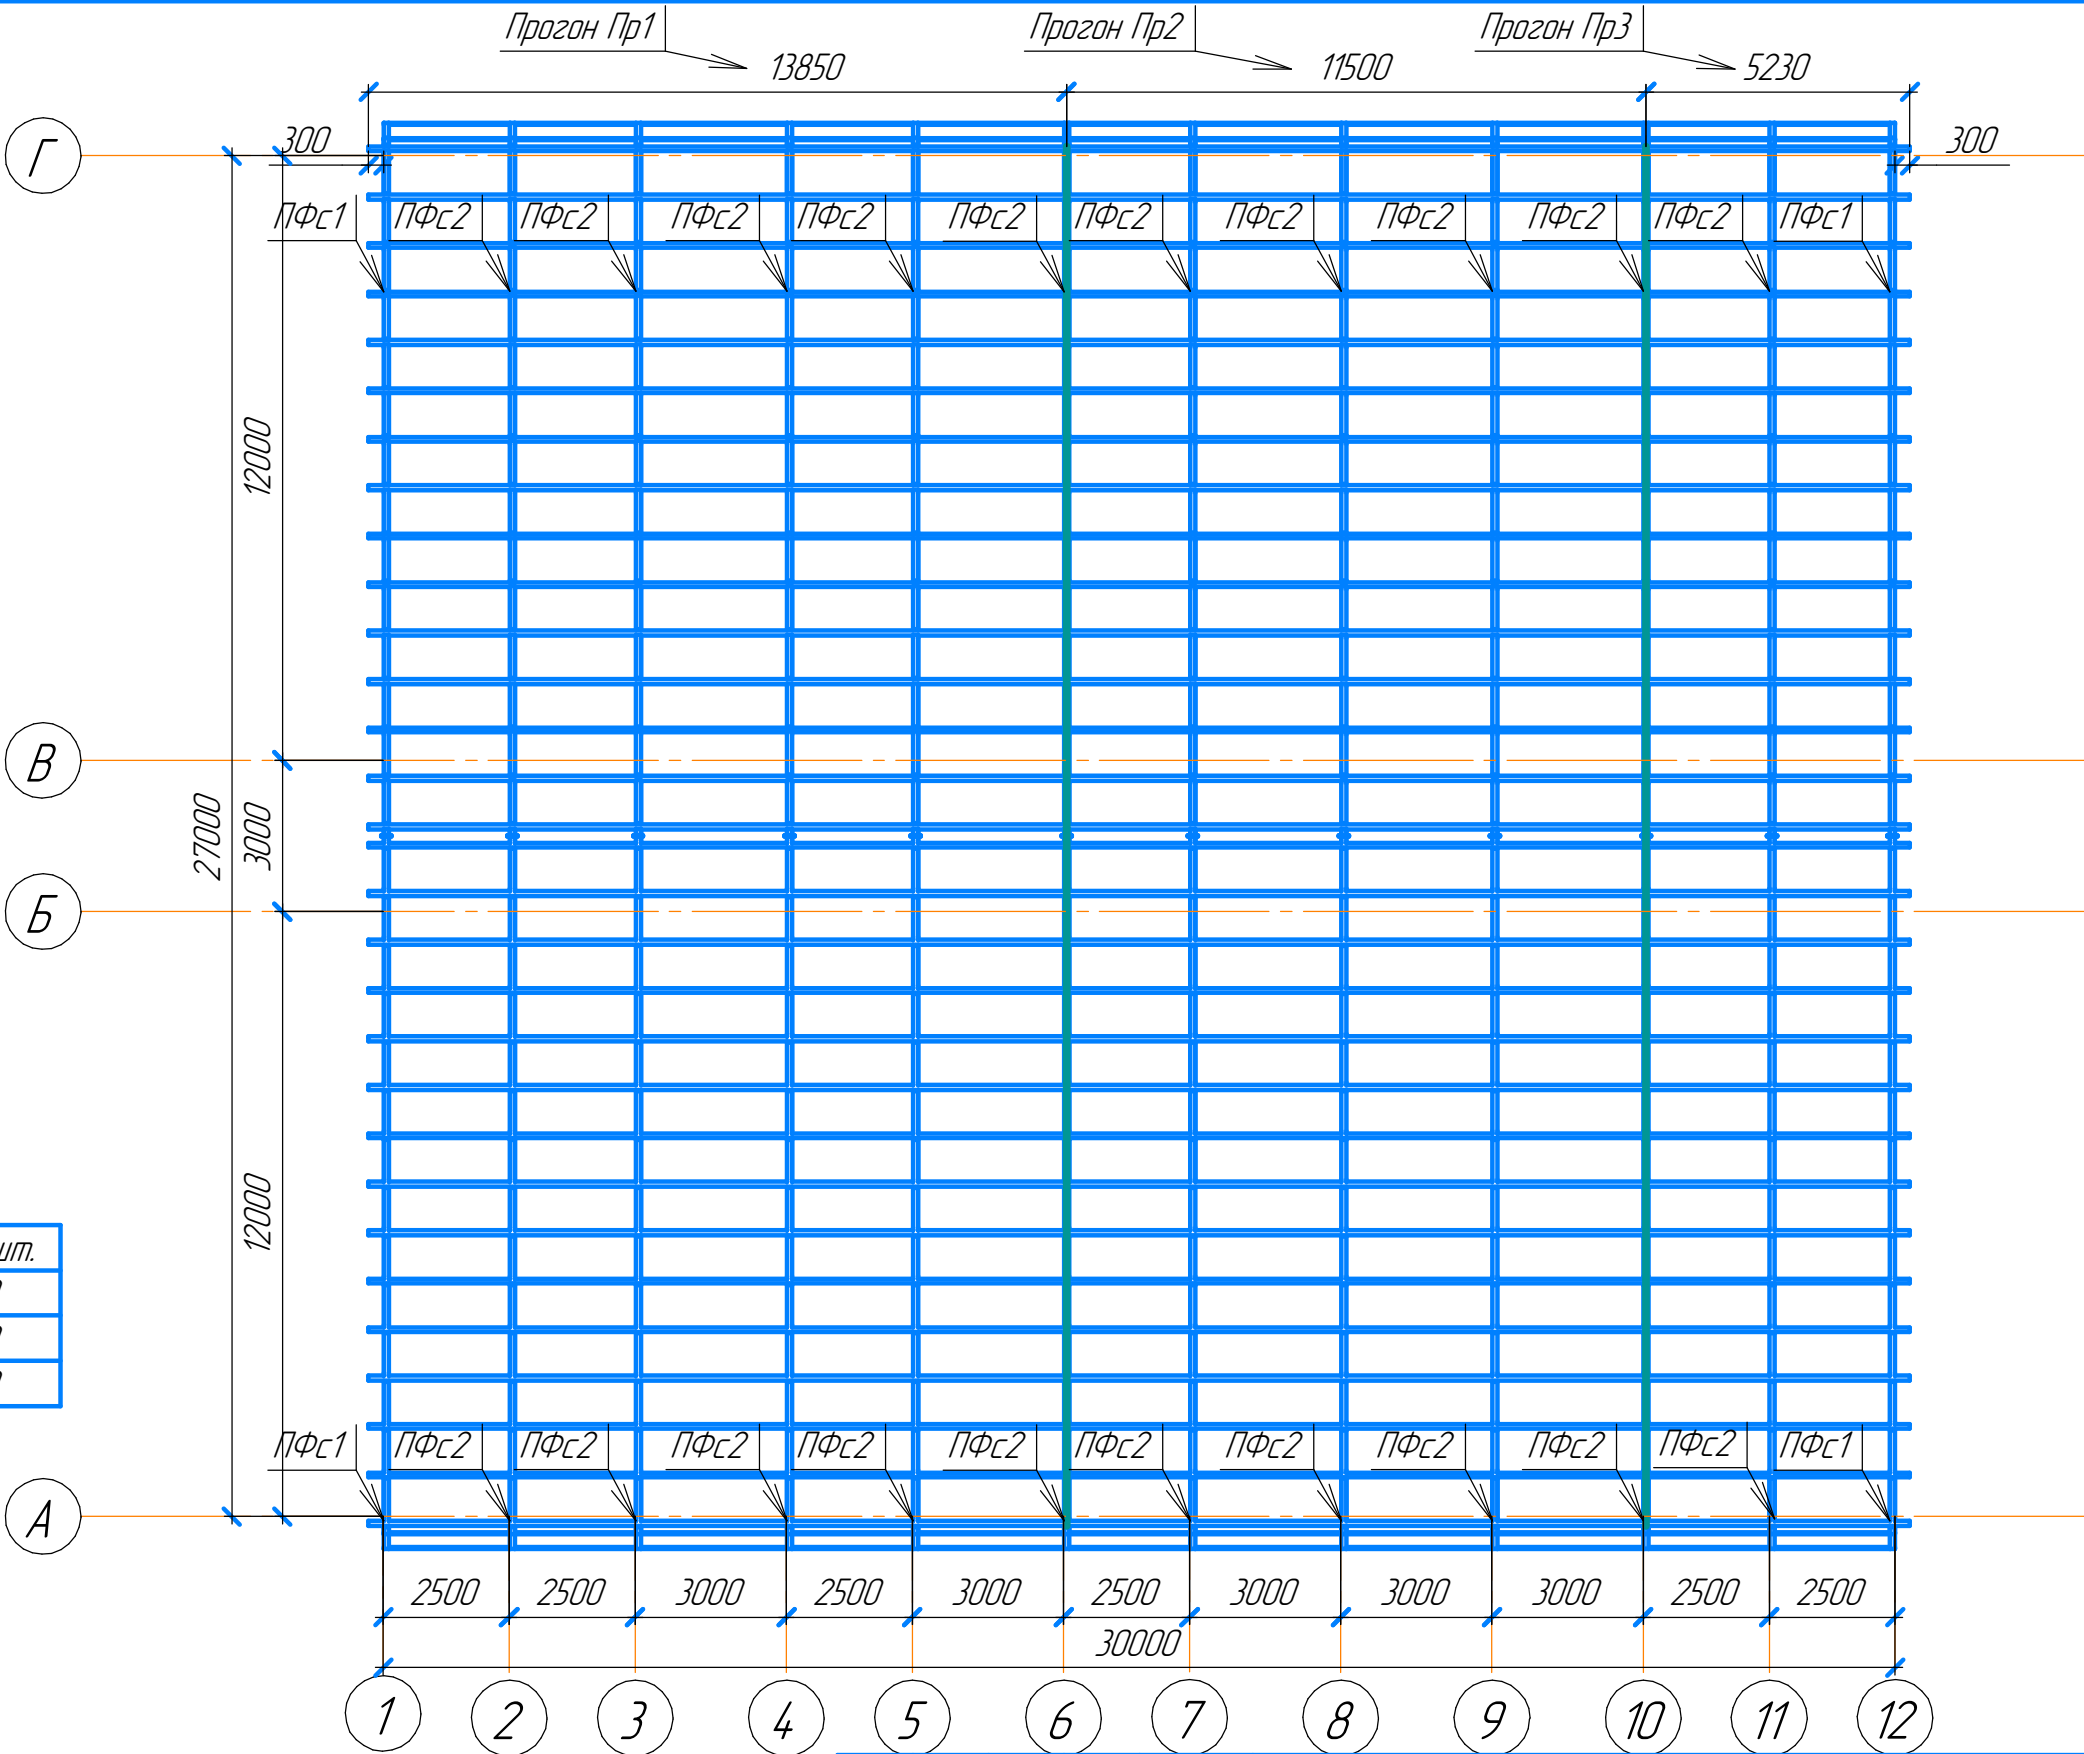


*фермы в проушинах блок-контейнеров закрепить с помощью электро-дуговой сварки

*прогоны в проушинах ферм закрепить с помощью электро-дуговой сварки

02-26 МЗ-УТЦ АР					
Здание мобильное МЗ-22 30100x27100x10180					
Изм.	Кол.уч.	Лист	№ док.	Подп.	Дата
Разработал	Терюшов О.В.				02.26
Проверил	Скасырских Е.А.				
Утвердил	Хамуряк А.В.				
Учебно-тренинговый центр				Стадия	Лист
Схема расстановки ферм и прогонов				9	Листов
				ООО "ТЕХНОВЕКТОР"	




План кровли

Схема крепления анкерной линии к прогону сквозь кровлю.

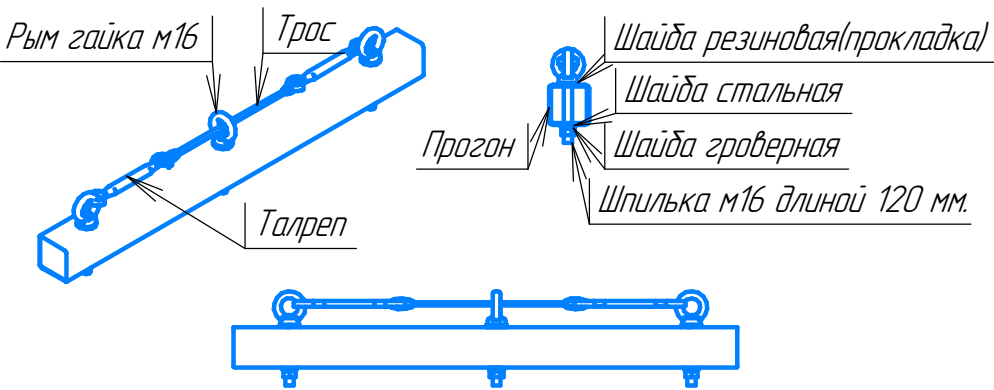


*возможны корректировки при монтаже

Обоз.	Наименование	Размер	Кол. шт.
Пл1	Профилированный лист НС 44	14790x1000	62
Пл2	Профилированный лист С 20	2725x1000	6
Пл3	Профилированный лист С 20	2220x1000	9

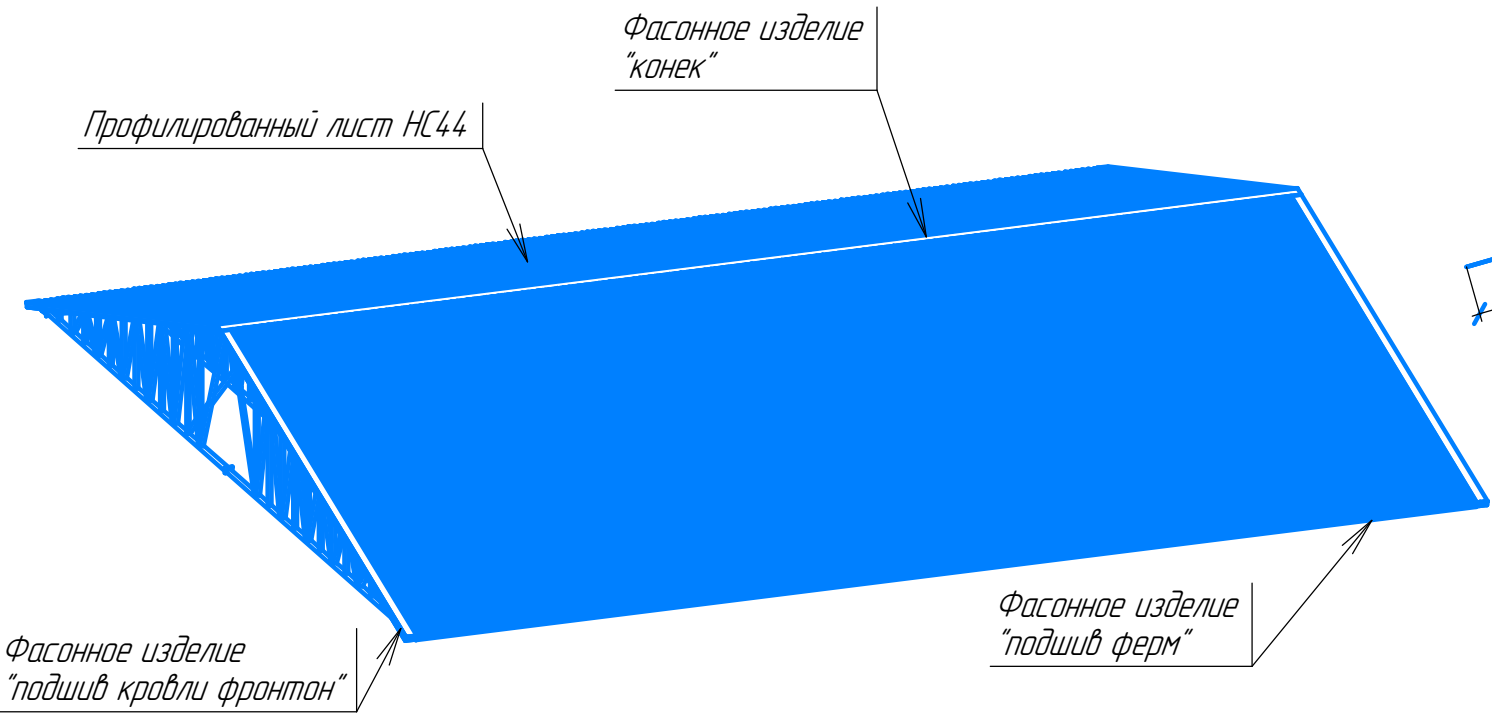
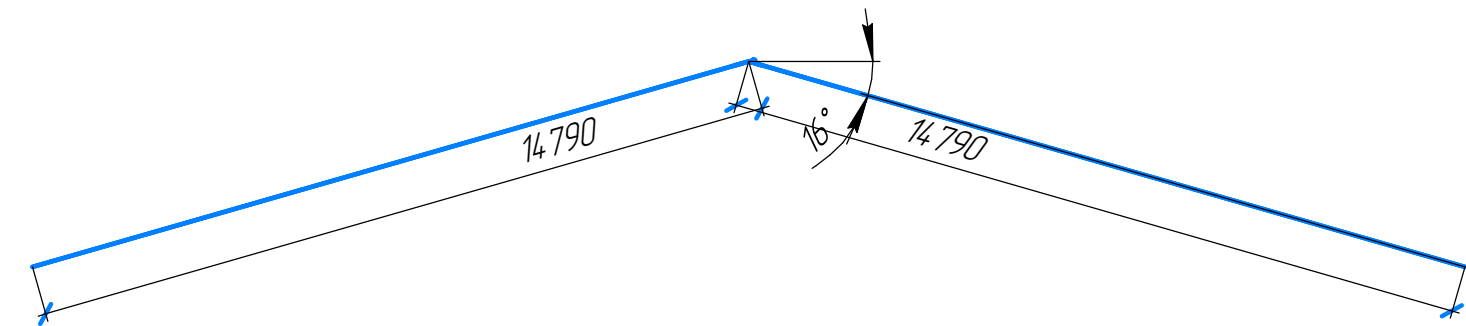
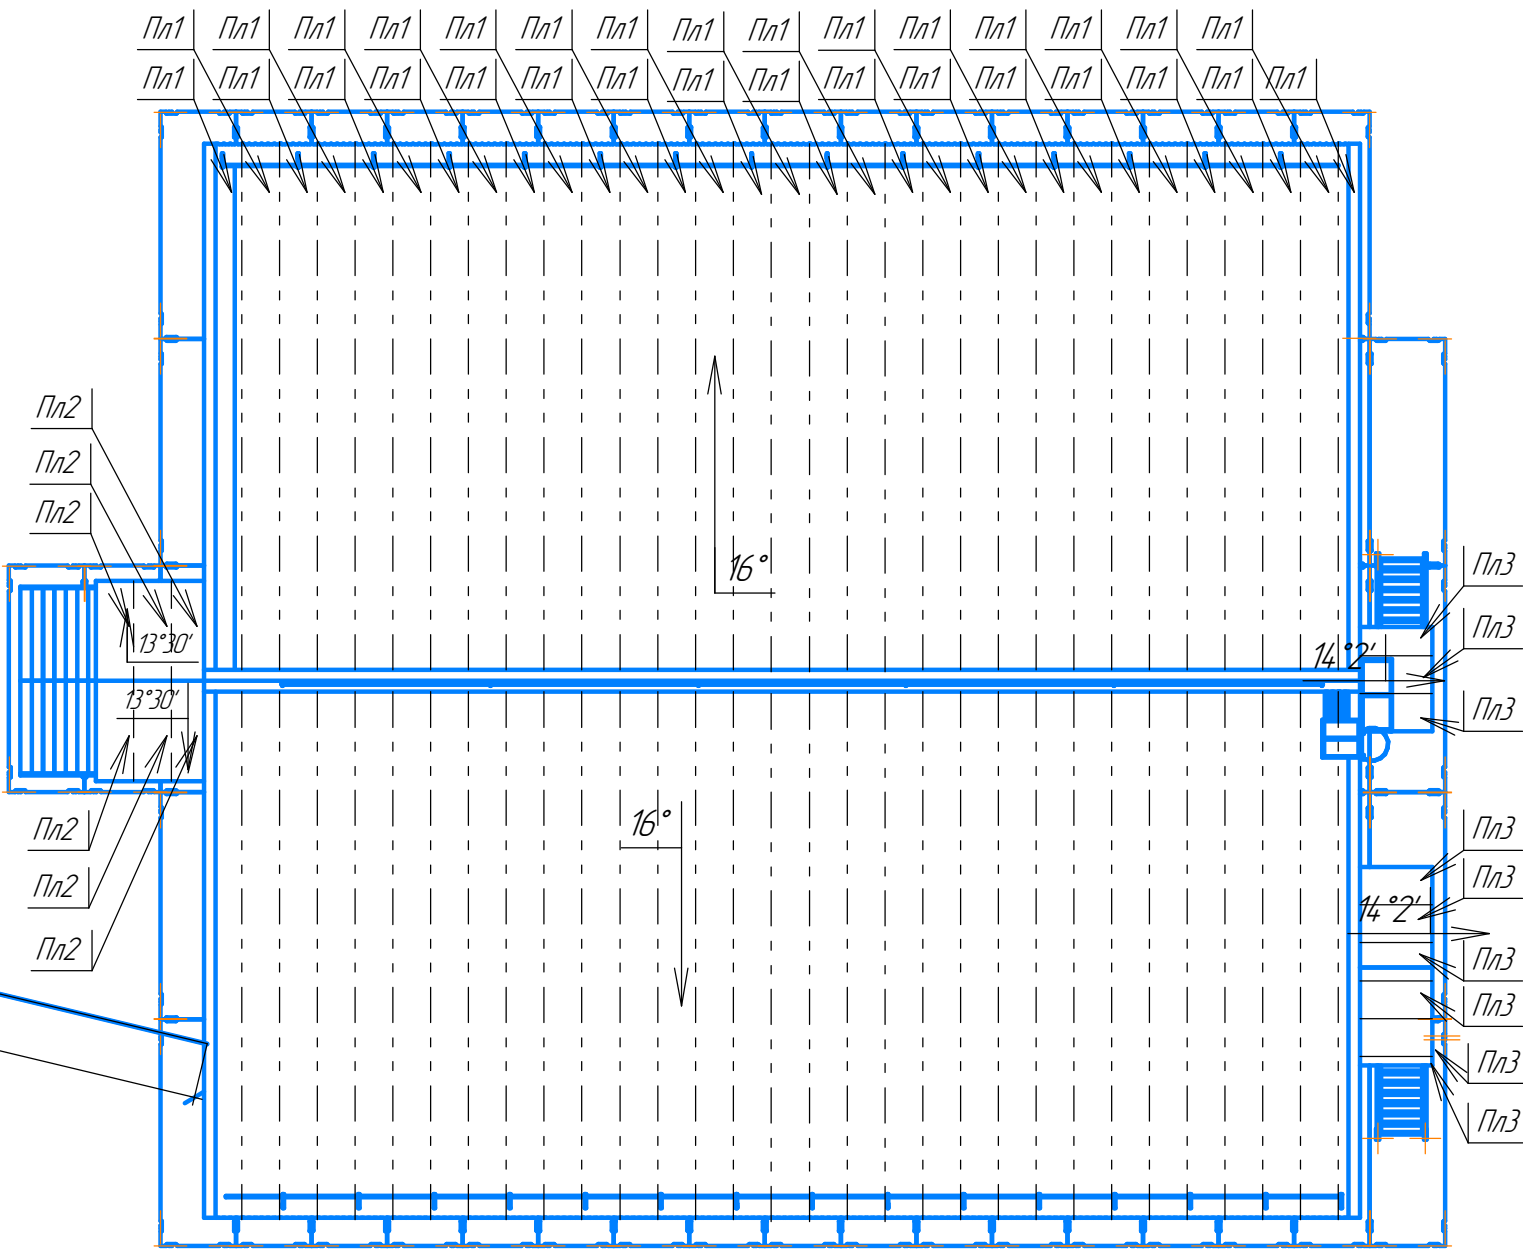


						02-26 МЗ-УТЦ АР			
						Здание мобильное МЗ-22 30100x27100x10180			
Изм.	Кол.уч.	Лист	№ док.	Подп.	Дата	Учебно-тренинговый центр	Стадия	Лист	Листов
Разработал	Терюшов О.В.				02.26			10	
Проверил	Скасырских Е.А.					План кровли	ООО "ТЕХНОВЕКТОР"		
Утвердил	Хамурык А.В.								

Схема укладки греющего кабеля под кровлю

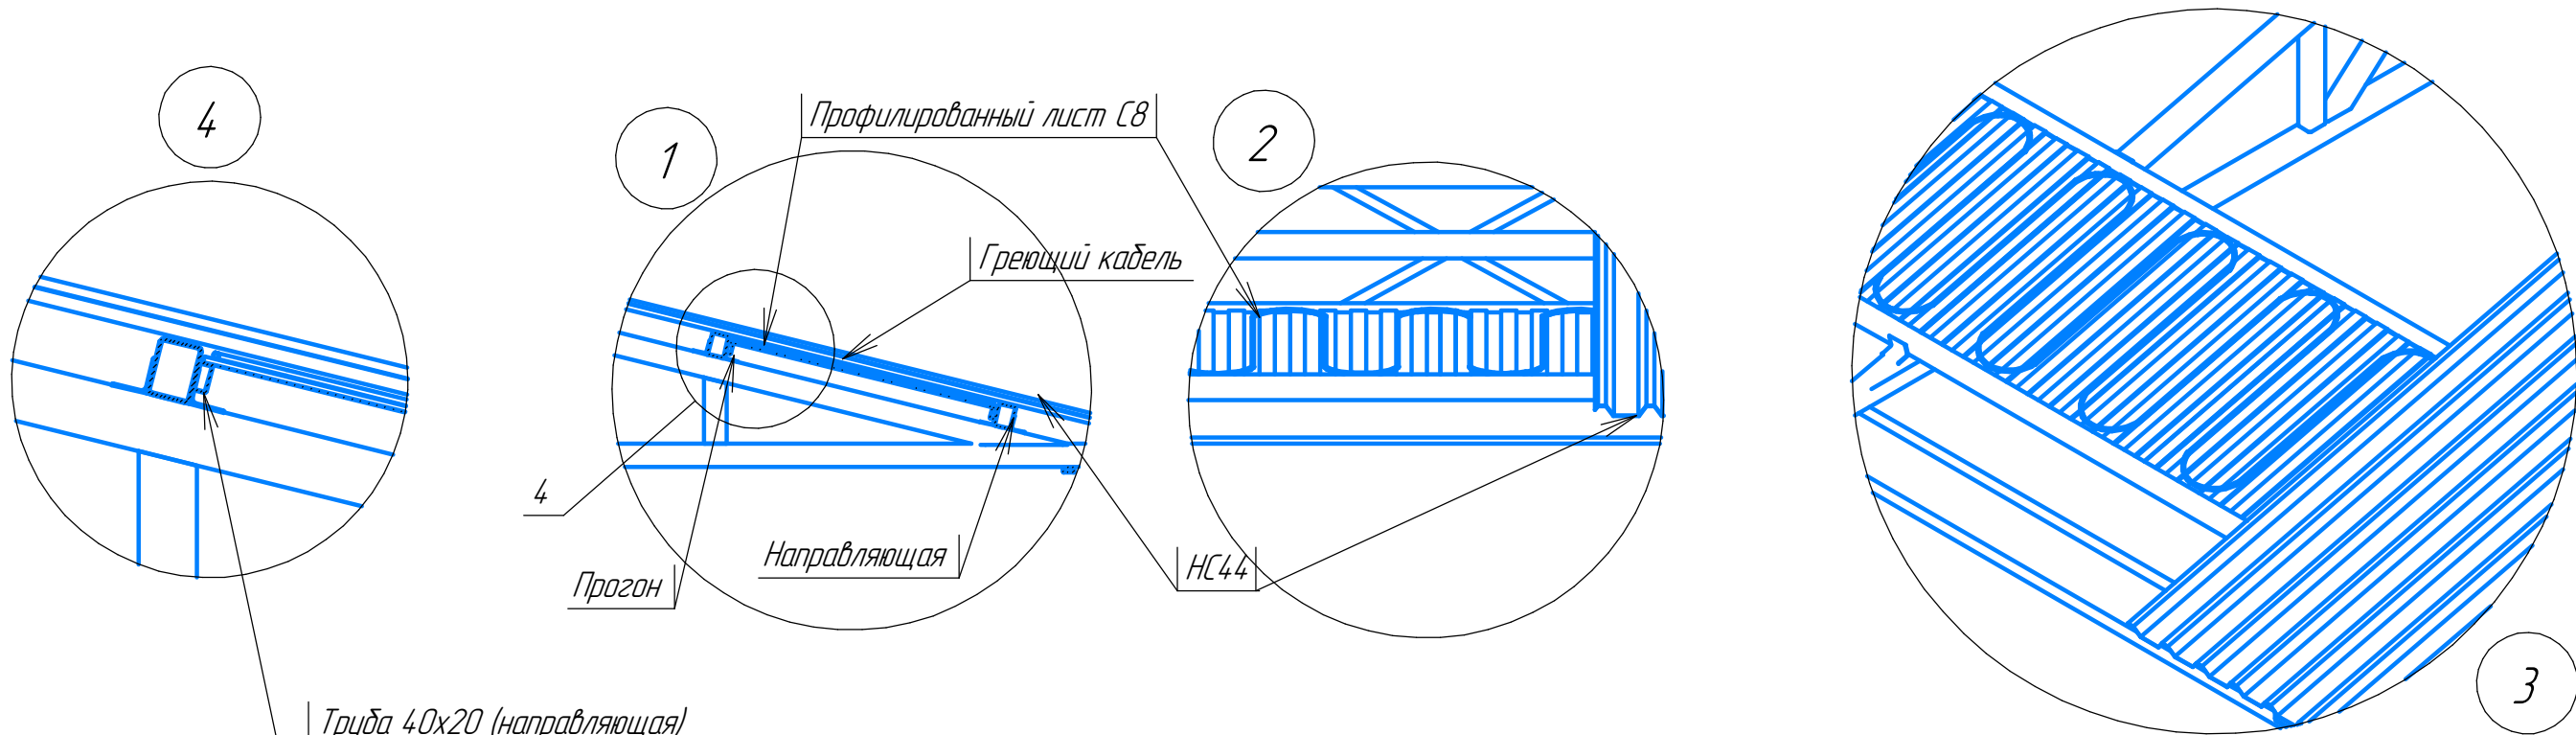


Труба 40х20 (направляющая)
-прикрутить к прогонам саморезами с отступом от верхней плоскости прогона 10мм.
Профилированный лист С8- закрепить саморезами к направляющим (40х20)
Греющий кабель закрепить клипсами к профилированному листу С8
Ширина обогрева ската не менее 500 мм.

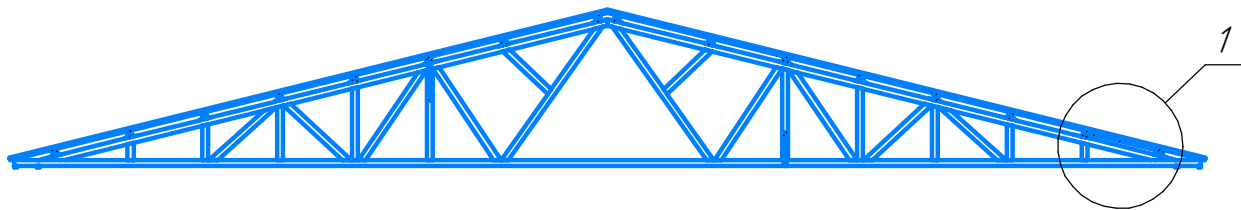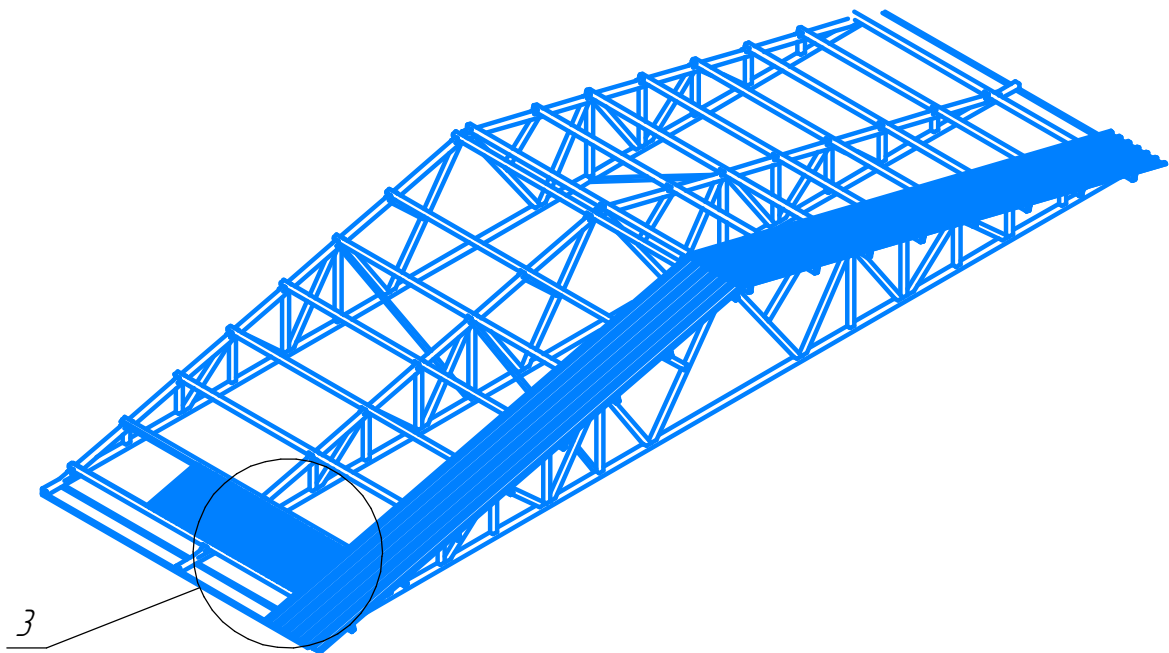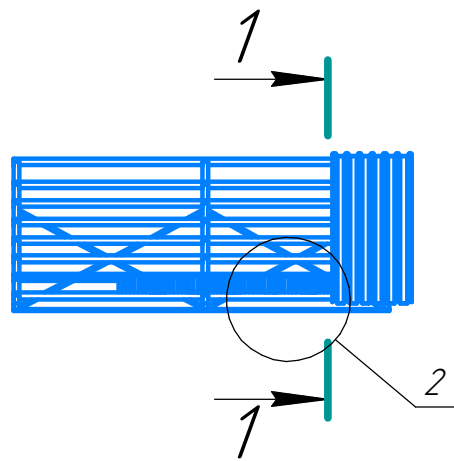

						02-26 МЗ-УТЦ АР		
						Здание мобильное МЗ-22 30100х27100х10180		
Изм.	Кол.уч.	Лист	№ док.	Подп.	Дата	Учебно-тренинговый центр	Стадия	Лист
Разработал	Терюшов О.В.				02.26			11
Проверил	Скасырских Е.А.					Схема укладки греющего кабеля под кровлю	ООО "ТЕХНОВЕКТОР"	
Утвердил	Хамуряк А.В.							

План на отметке 0,000

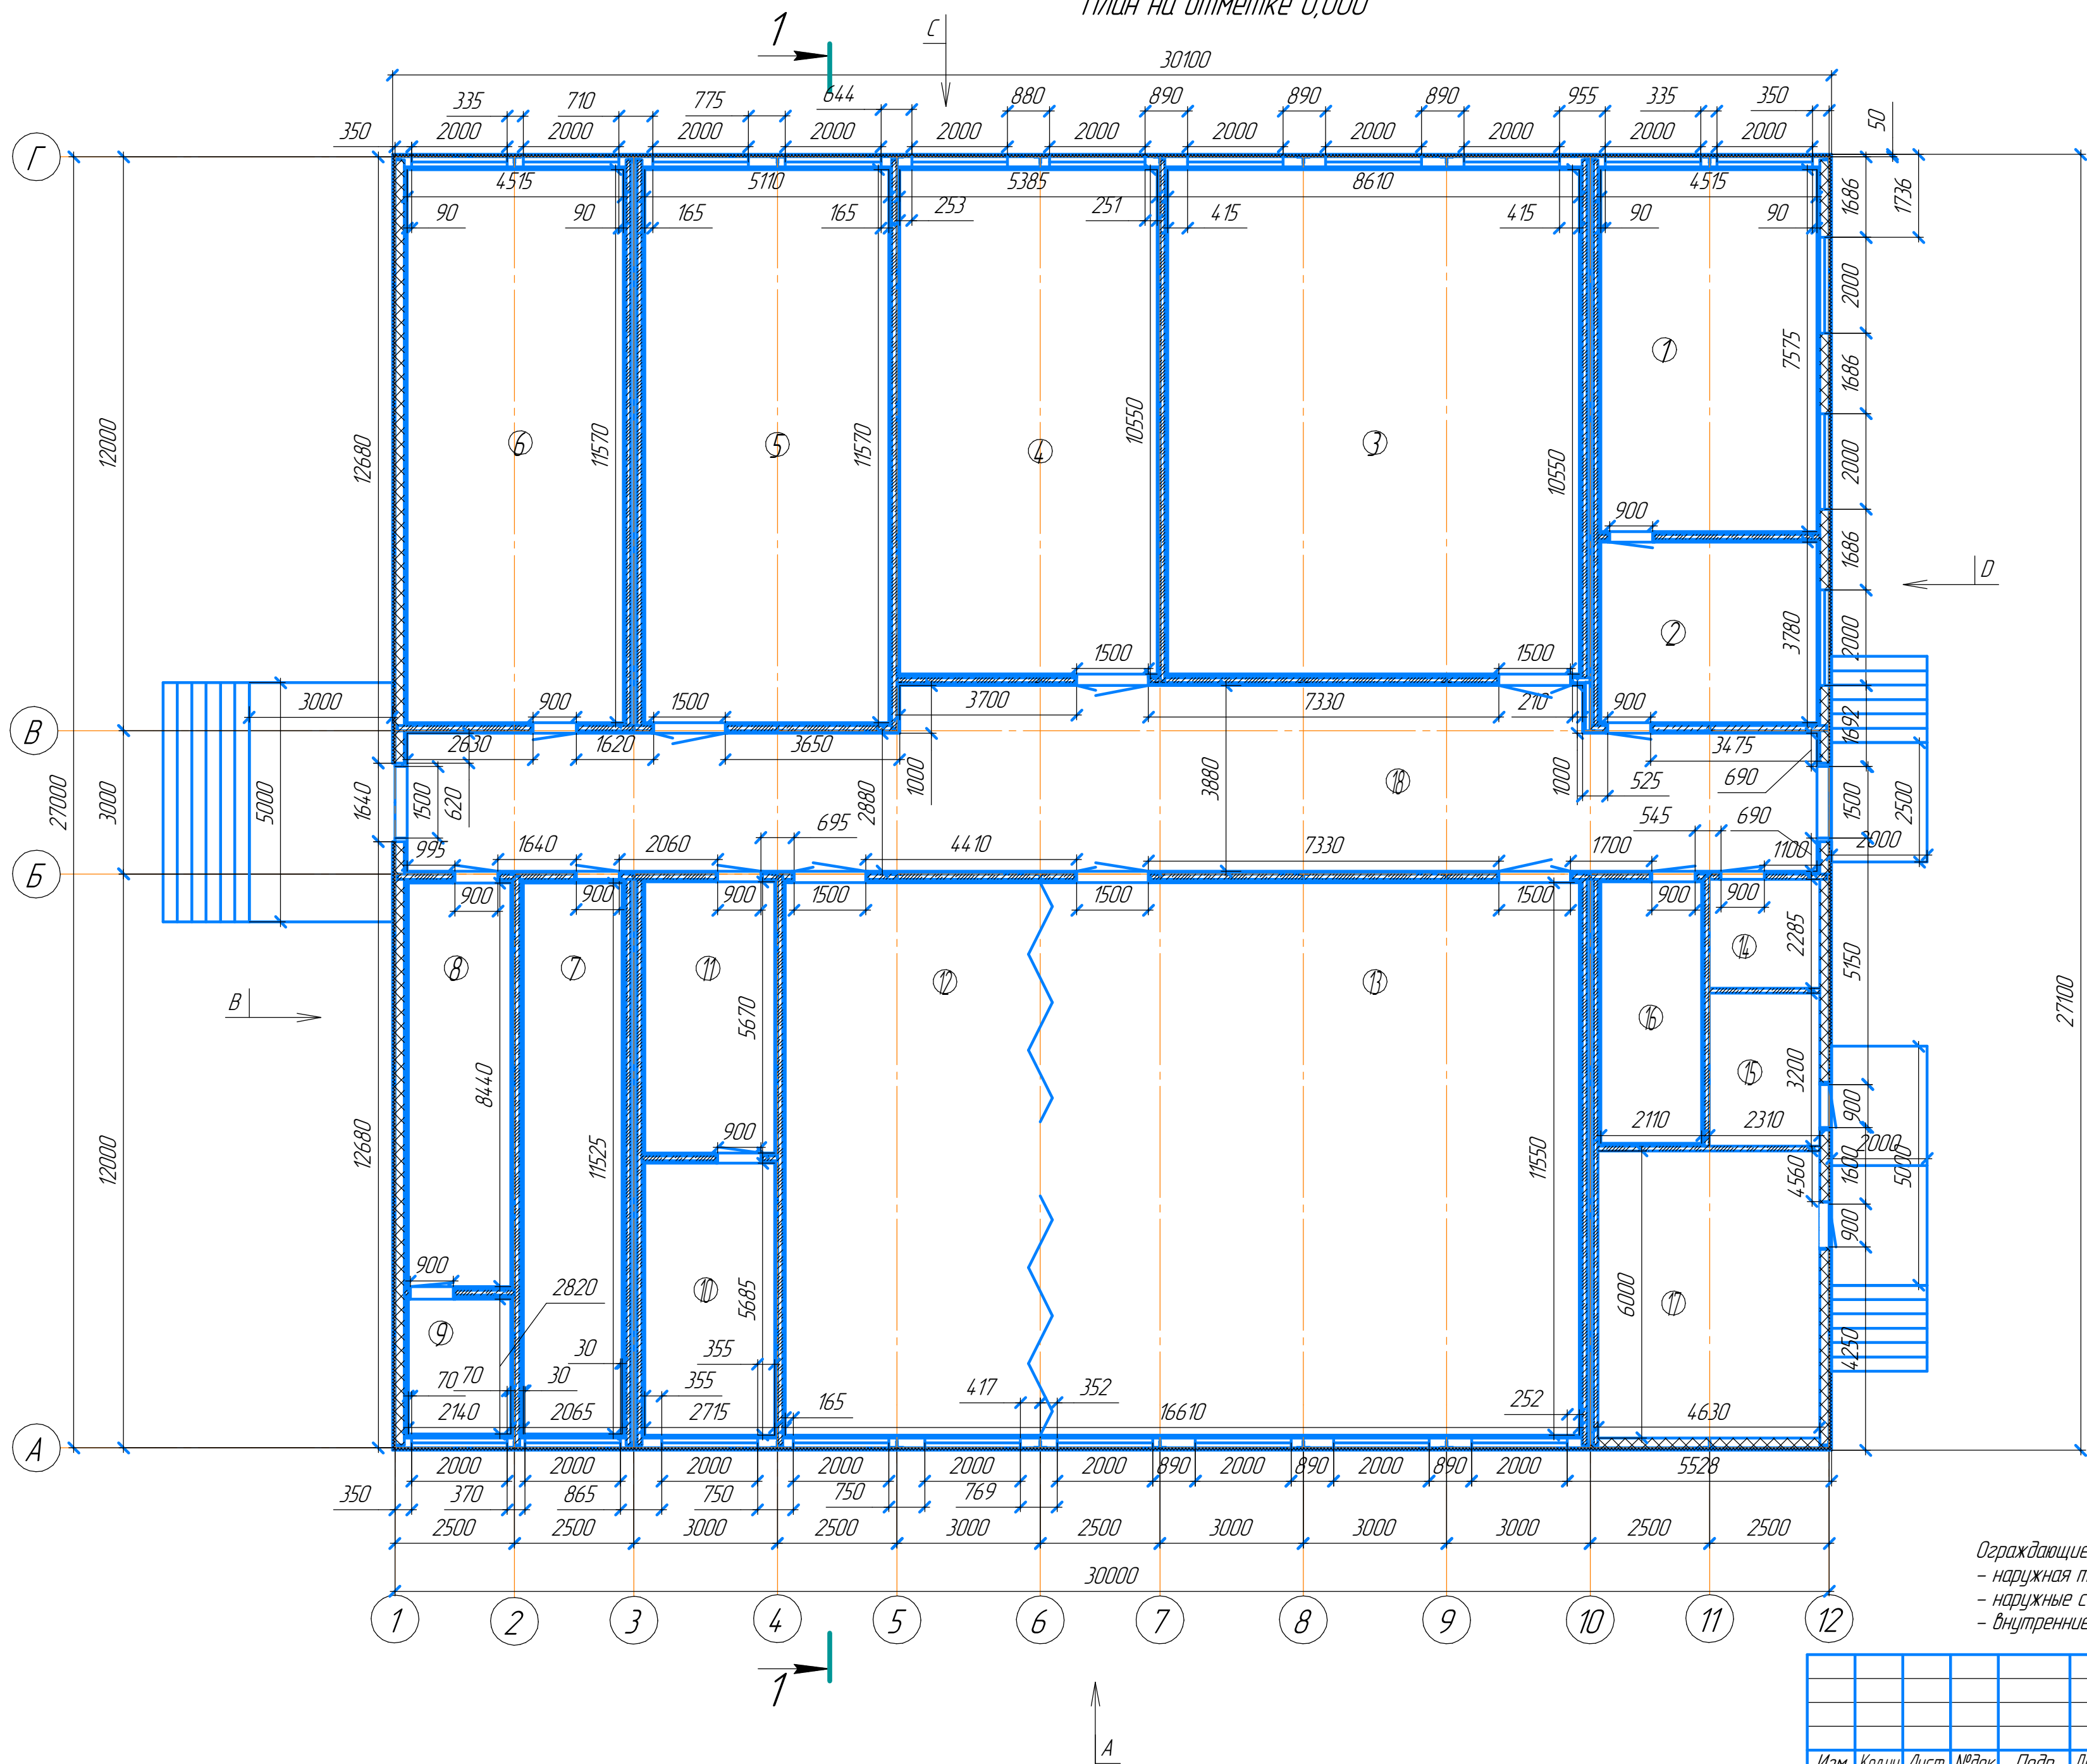

Экспликация помещений			
№	Наименование	S=м2	Примечание
1	Кабинет специалистов УТЦ	34.20	
2	Кабинет преподавателей	17.06	
3	Класс ПК	90.84	
4	Класс ТЭС ЧЭЦН	56.81	
5	Класс корп. обучения №3	59.08	
6	Гардероб	52.24	
7	Санузел мужской	23.78	
8	Санузел женский	18.06	
9	Тех. помещение	6.04	
10	Склад хранения СИЗ РВ	15.43	
11	Раздевалка спецодежда	15.39	
12	Класс корп. обучения №2	61.62	
13	Класс корп. обучения №1	130.24	
14	Серверная	5.27	
15	Электрощитовая	7.38	
16	Склад-Архив УТЦ	11.52	
17	ИТП	27.79	
18	Коридор	99.31	
		Общая S = 732.06 м2	

Стены наружные
сэндвич панель трехслойная,
базальтовое наполнение,
облицовка оцинкованным листом
Толщина панели 200 мм.

Стены внутренние
сэндвич панель трехслойная,
базальтовое наполнение,
облицовка оцинкованным листом
Толщина панели 100 мм.

1-Стены наружные
сэндвич панель трехслойная,
базальтовое наполнение,
облицовка оцинкованным листом
Толщина панели 50 мм.
2-Фасонные изделия 50 мм.
(гибочный элемент)

Ограждающие конструкции (стен/перегородок). Панели типа «Сэндвич»:
- наружная толщина металла 0,7мм, внутренняя 0,5мм,
- наружные стены из панелей металлических трехслойных ПТС- У 200мм,
- внутренние из панелей металлических трехслойных ПТС- У 100мм,

02-26 МЗ-УТЦ АР

Здание мобильное МЗ-22
30100x27100x10180

Учебно-тренинговый центр

План на отметке 0,000

Формат А2

*размер монтажного дверного проема уточнить по двери.

Согласовано	
Изм. №	
Взам. инв. №	
Подп. и дата	
Инв. № подл.	

Изм.	Колуч.	Лист	№ док.	Подп.	Дата
Разработал	Терюшов О.В.				02.26
Проверил	Скосьевских Е.А.				
Утвердил	Хамурьяк А.В.				

Схема расстановки оборудования



Спецификация оборудования

Модель – *цвет согласно дизайн проекта.

- Учебные классы
- 1 – Стул с пюпитром. – 120 шт.
Материал – металлический каркас, плоскоовальная металлическая труба, спинка/сидение/подлокотники – дерево
Кабинеты. Учебные классы.
- 2 – Стол рабочий – ШхГхВ 1600х800х775мм, – 36 шт.
– столешница ДСП 25мм
– цвет дуб медовый, кромка ABS 2мм,
– вывод проводов – проводник SISQ,
– опоры А-образные металлические прямоугольного сечения 60*30 мм, регулируемые по высоте с учетом неровностей пола,
– цвет опор белый
Экран 1400х400 мм, уровень ниже стола, материл ДСП, s=16 мм, противоударная кромка ABS 1мм, цвет дуб медовый, в комплекте крепление.
Кабинеты. Учебный классы.
- 3 – Тумба модульная – ШхГхВ 404х496х616мм 3 ящика, – 10 шт.
материал каркаса и ящиков ДСП 16мм, кромка ABS 1мм,
– цвет корпуса белый, цвет фасадов дуб медовый,
– опоры колесные с прорезиненной основой, направляющие металлические роликовые с плавным ходом, ручки металл серебра.
Кабинеты. Учебный классы.
- 4 – Тумба под оргтехнику – ШхГхВ 800х600х570мм, – 3 шт.
каркас ДСП 16мм цвет белый, кромка ABS 1мм,
– топ ДСП 22мм цвет белый, кромка ABS 2мм,
– фасад ДСП 16мм цвет дуб медовый, ручки металл серебра
Кабинеты.Учебный классы.
- 5 – Тумба-купе под самоспасатели – 1600х400х1150 мм, – 6 шт.
каркас ДСП 16мм цвет белый, кромка ABS 2 мм,
– топ ДСП 25мм цвет белый, кромка ABS 2мм,
– фасад ДСП цвет дуб медовый, ручки металл серебра.
Кабинеты. Учебный классы.
- 6 – Шкаф для одежды – ШхГхВ 800х600х1944мм, – 5 шт.
каркас ДСП 16мм, кромка ABS 2мм, цвет белый,
материал топа/фасада ДСП 25мм, кромка ABS 2мм, цвет дуб медовый, две полки + выдвигаемая вешалка, ручки металл цвет серебра.
Кабинеты. Учебный классы.
- 7 – Шкаф для документов – 800х400х1944 мм – 5 шт.
каркас ДСП 16 мм, кромка ABS 1мм, цвет белый,
материал топа, фасада ДСП 25 мм, кромка ABS 2 мм, цвет дуб медовый, нижние и верхние дверцы ДСП, между дверцами ниша, ручки металл, цвет серебра.
Кабинеты. Учебный классы.
- 8 – Шкаф для документов – 800х400х1944 мм, – 1 шт.
каркас ДСП 16 мм, кромка ABS 1 мм, цвет белый,
материал топа, фасада ДСП 25 мм, кромка ABS 2 мм, цвет дуб медовый, нижние дверцы ДСП, верхние стекло, ручки металл, цвет серебра
Кабинеты. Учебный классы.
- 9 – Компьютерное кресло: – 54 шт.
Материал сидения – сетка, материал каркаса – пластик, цвет обивки – серый, цвет ножек – белый.
Коридор.
- 10 – Многоместная скамья – 4 шт.
Размер,мм – 1815х670х923, труба Ш19мм, пл/овальная труба 50х30мм, 30х15мм, лист S=1мм, пластиковые заглушки и опоры, с мягкими накладками на подлокотниках.
Гардероб. Раздевалка.
- 11 – Вешалка напольная для одежды в комплекте с плечиками. – –33 шт.
Склад архив.
- 12 – Стеллаж для архива металлический. – 5 шт.
Конструкция стеллажа выстраиваемая.
Покрытие на уголках, гайках и болтах оцинкованное.
Количество полок – 5 шт.
Глубина полок – 400 мм
Длина 2000 мм
Нагрузка на полку – 120 кг
Высота стеллажа – 2000 мм
Тип покрытия – порошковая краска. Цвет – серый полуматовый.

- Склад РВ
- 13 – Вешалка на ножках усиленная, для тяжелой одежды, – 4 шт.
с крючками двухсторонняя, 20 крючков.
Материал конструкции вешалки и крючков – металл хромированный.
Материал панели для крючков – ЛДСП с защитной кромкой из ПВХ.
Высота панелей регулируется.
Оборудование. Цвет согласно дизайн проекта.
Классы обучения
- ТВ – Панели – Диагональ (98 дюймов) – 1 шт.
Диагональ (86 дюймов) – 3 шт. – *предоставляет заказчик
Диагональ (65 дюймов) – 2 шт.
Коридор
- 16 – Пурифайер напольного типа – 1 шт.
с ультрафильтрационной системой очистки воды.
1. Бак холодной воды 6,5л.
2. Бак горячей воды 5л.
3. Мощность нагревательного элемента 800Вт.
4. Защита на крапе горячей воды.
5. Краны “нажим кружкой”.
6. Производительность г/в: 6,5л/ч(85–92С°), х/в: 3,5л/ч(5–10С°)
Габариты без упаковки (ВхШхГ) 1120х320х357 мм
Санузлы.
- 17 – Унитаз-компакт с бачком, горизонтальный тип выпуска, – 7 шт.
режим слива с 2 кнопками, материал: санфарфор.
- 17,1 – Писсуар – 4шт
- 18 – Раковина круглая накладная, тип установки на столешнице, – 6 шт.
материал – санфарфор, цвет белый
- 19 – Смеситель для раковины чаши цвет – хром – 6 шт.
с гибкой подводкой и креплением
Санузлы
Гардероб
Раздевалка спецодежды
- 20 – Зеркало прямоугольное, настенной установки, размер 1200х600 – 4 шт.
Санузлы
- 21 – Настенный диспенсер для жидкого мыла механический, объём 1000 мл. – 2 шт.
Материал отделки – нержавеющая сталь
Размер диспенсера – 23,1410,7411,5 см, цвет: серебристый, матовый
Санузлы
- 22 – Туалетные перегородки глухие от пола до потолка. – 7 шт.
Материал – ЛДСП, цвет согласно дизайна
Санузлы
- 23 – Высокоскоростная сушилка для рук.
Антивандальный корпус, бесконтактное управление, HEPA фильтр и UV обеззараживание.
Автоматическое отключение, степень защиты IPX4
Размер, мм: 730х222х300, цвет: матовая сталь
Прочие конструкции.
- 24 – Грязезащитная решетка – размер: 1200мм х 800 мм 2шт.

- Двери.
- *размер монтажного проема уточнить по двери.
- Д1 – Входные двери. Правые – 2 шт.
Двери алюминиевые, с остеклением, с уплотнителем, доводчиками для самозакрывания, размер ШхВ в свету, мм: 1500х2000 цвет профиля графит (RAL 7024).
- Д2 – Серверная. Правая–1 шт.
Однопольная, глухая, металлическая противопожарная дверь.
Класс огнестойкости EI-60.
Используемая сталь – холоднокатаный лист толщиной не менее 1,5 мм
Отделка двери – порошковое напыление антивандальное, вентиляционная решетка, размер ШхВ в свету, мм: 900х2000, цвет: серый (RAL 7024)
- Д3* – ИТП. Электрощитовая. Левые – 2 шт.
Однопольная, глухая, металлическая дверь.
Используемая сталь – холоднокатаный лист толщиной не менее 1,5 мм
Отделка двери – порошковое напыление, антивандальное, вентиляционная решетка, размер ШхВ в свету, мм: 900х2000, цвет: серый (RAL 7024)
Внутренние двери.
- Учебные классы
- Д4 – Алюминиевые двери, матовое остекление, холодный профиль, Правые – 3 шт. *Левые – 3 шт.
цвет – серый (RAL 7024), цвет фурнитуры: серый (RAL 7024)
размер ШхВ в свету, мм: 1500х2000
Кабинеты. Вспомогательные помещения.
- Д5 – Алюминиевые двери, матовое остекление, холодный профиль, Правые – 3 шт. *Левые – 6 шт.
цвет: серый (RAL 7024), цвет фурнитуры: серый (RAL 7024)
размер ШхВ в свету, мм: 900х2000

- Окна.
- Ок1 – Окна размер, мм (ШхВ): 2000х2400, профиль 70мм (типа Экспроф), – 23 шт.
толщина стп. 40мм (двухкамерный) цвет: наружный (RAL 7024), внутренний (RAL 9010)
*окна следует расположить симметрично, выдерживая равные расстояния от пола и потолка.
- Жалюзи
- 25 – Светонепроницаемые рулонные, шторы Black Out, кассетные. – 23 шт.

* оборудование поставляется по заказу заказчика или аналог

							02-26 МЗ-УТЦ АР			
							Здание мобильное МЗ-22 30100х27100х10180			
Изм.	Колуч.	Лист	№ док.	Подп.	Дата		Учебно-тренинговый центр	Стадия	Лист	Листов
Разработал	Терюшов О.В.				02.26				14	
Проверил	Скасьерских Е.А.						Спецификация оборудования	ООО"ТЕХНОВЕКТОР"		
Утвердил	Хамуряк А.В.									

Схема расстановки сэндвич-панелей

Страна А

Страна В

Трехслойная сэндвич-панель (стенная)
ТСП-З-200-1000-Т-Т-МВ
ГОСТ 32603-2021 класс 2
(ПЗ-01-07\ПЗ-01-9010-0.5)

Трехслойная сэндвич-панель (перегородочная)
ТСП-З-100-1000-Т-Т-МВ
ГОСТ 32603-2021 класс 2
(ПЗ-01-05\ПЗ-01-9010-0.5)

Трехслойная сэндвич-панель
ТСП-З-200-1000-Т-Т-МВ
ГОСТ 32603-2021 класс 2
(ПЗ-01-07\ПЗ-01-9010-0.5)

Страна С

Страна D

Сэндвич-панель перегородочная

Наименование	Размер	Кол.шт.
Сэндвич-панель	2020x1000x200	23
Сэндвич-панель	4420x1000x200	81
Сэндвич-панель	2315x1000x200	2
Сэндвич-панель	2420x1000x200	324
Сэндвич-панель	2920x1000x200	270
Сэндвич-панель перегородочная	4420x1000x100	144
Сэндвич-панель перегородочная	4370x1000x100	76

Схема расстановки сэндвич панелей верх-низ
на один блок контейнер длина панели 2500мм. - 6 блоков



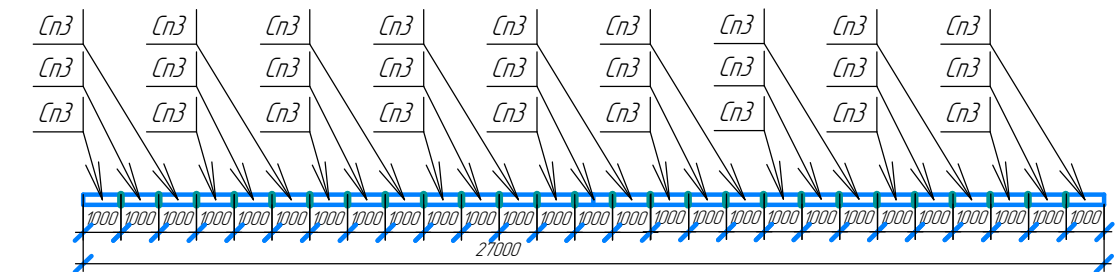


Схема расстановки сэндвич панелей верх-низ
на один блок контейнер длина панели 3000мм. - 5 блоков

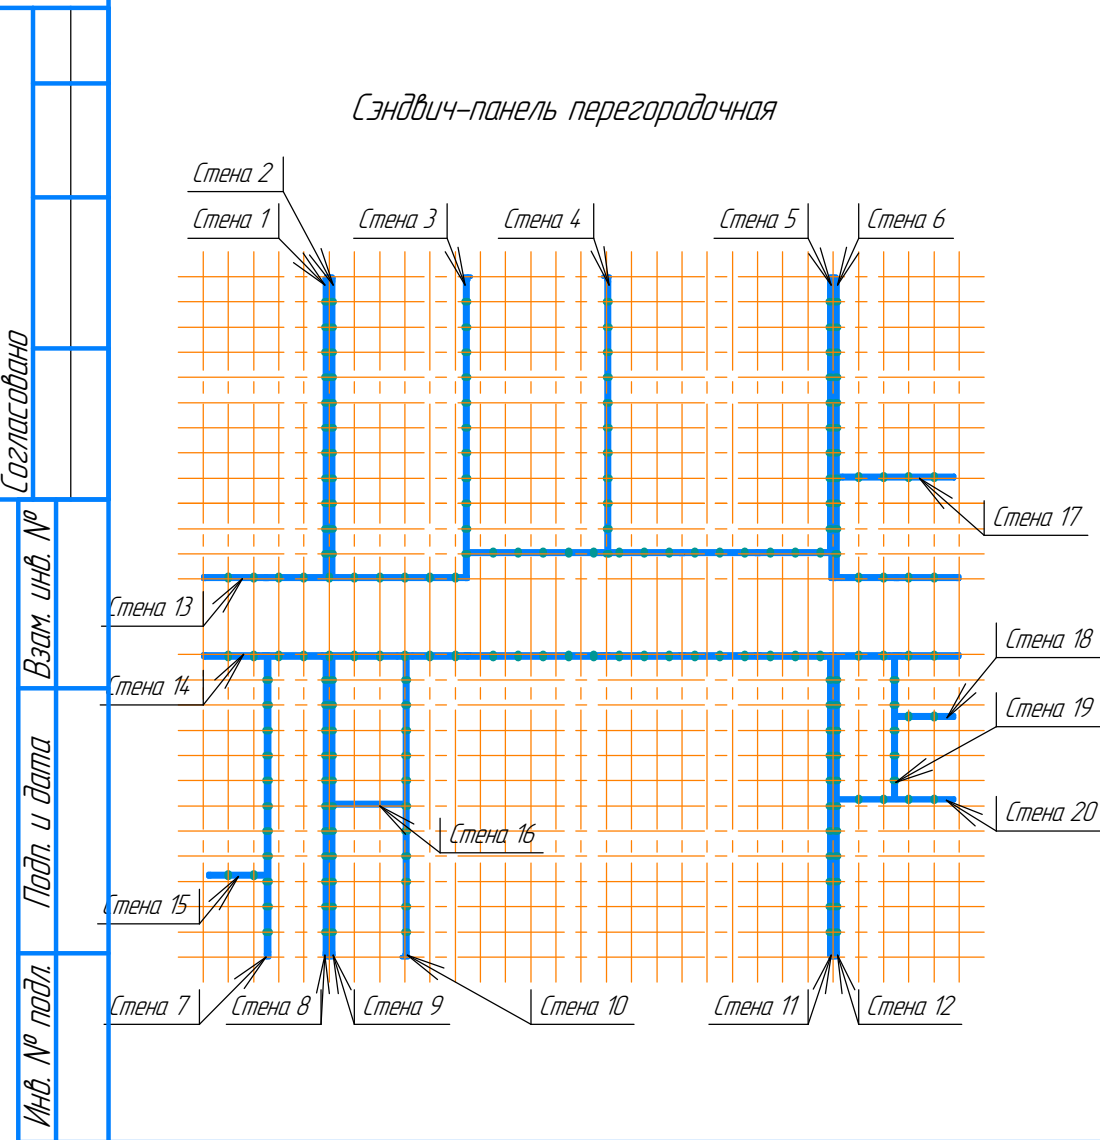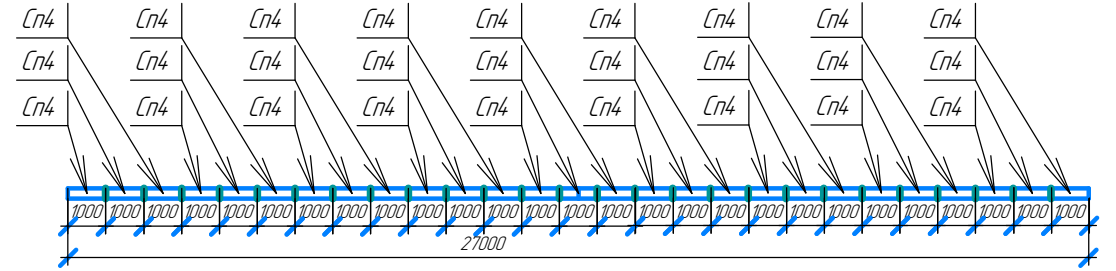

						02-26 МЗ-УТЦ АР		
						Здание мобильное МЗ-22 30100x27100x10180		
Изм.	Кол.уч.	Лист	№ док.	Подп.	Дата			
Разработал	Терюшов О.В.				02.26	Учебно-тренинговый центр	Стадия	Лист
								Листов
								15
Проверил	Скасырских Е.А.					Схема расстановки сэндвич-панелей	ООО "ТЕХНОВЕКТОР"	
Утвердил	Хамуряк А.В.							

Спецификация

Поз.	Наименование	шт.	Кол.	Разм.	Масса кг.	Примечание
Элементы здания						
	Подрамник ПР 1	шт.	6	16000х3000х1000	6540	
	Подрамник ПР 2	шт.	6	14000х3000х1000	5670	
	Перемычка тех. подполье Св1, Св2, Св3, Св4, Св5	шт.	18	2000,1000,3000,х1000	1800	
	Низ Блок контейнера	шт.	12	2500х13500х4 980	2500	
	Верх Блок контейнера	шт.	12	2500х13500х4 980	2000	
	Низ Блок контейнера	шт.	10	3000х13500х4 980	3000	
	Верх Блок контейнера	шт.	10	3000х13500х4 980	2500	
	Полу-Фермы	шт.	24	14 150х4 080	20400	
	Прогоны Пр 1	шт.	30	80х80х13850	3840	
	Прогоны Пр 2	шт.	30	80х80х11500	3180	
	Прогоны Пр 3	шт.	30	80х80х5230	1470	
	Проф.лист НС44(кров.)	шт.	62	14 790х1000х0.7		
	Проф.лист С8	шт.	60	900х1150х0.45		для гр-го кабеля
	Проф.лист С 20 (входная группа центр)	шт.	6	2725х100х0.45		
	Проф.лист С 20 (входная группа)	шт.	9	2220х1000х0.45		
	Входная группа центр	шт.	1	4000х3000х4 245	2030	
	Входная группа	шт.	3	2500х2000х3 930	1590	
	Дверь входная металлическая (противопожарная)	шт.	2	1550х2000		световой проем
	Дверь входная металлическая (противопожарная)	шт.	3	900х2000		световой проем
	Дверь внутренняя	шт.	6	1550х2000		световой проем
	Дверь внутренняя	шт.	9	800х2000		световой проем
	Окно поворот./откидное + москитная сетка	шт.	23	2000х2400		жалюзи
	Лестница на крышу	шт.	1	0.7х11.2	200	
	Анкерная линия	шт.	1			
	Снегозадержатели	комп.	30	2000		
	Желоб водосточный D125х3000	шт.	22			
	Труба водосточная D90х3000	шт.	16			
	Труба водосточная D90х1000	шт.	8			
	Держатель трубы D90	шт.	40			
	Держатель желоба карнизный D125х280	шт.	120			
	Заглушка желоба D125	шт.	4			
	Соединитель желоба D125	шт.	10			
	Воронка выпускная D125/90	шт.	8			
	Колено трубы D90х60 градус	шт.	8			
	Колено сливное D90	шт.	8			
	Саморегулирующийся кабель (водосток)	м/п		Расчет длины кабеля в разделе ЗОМ		
	Саморегулирующийся кабель (кровля)	м/п				

						02-26 МЗ-УТЦ АР			
						Здание мобильное МЗ-22 30100x27100x10180			
Изм.	Колуч.	Лист	№ док.	Подп.	Дата	Учебно-тренинговый центр	Стадия	Лист	Листов
Разработал		Терюшов О.В.			02.26			16	
Проверил		Скасырских Е.А.				Спецификация	ООО "ТЕХНОВЕКТОР"		
Утвердил		Хамуряк А.В.							